



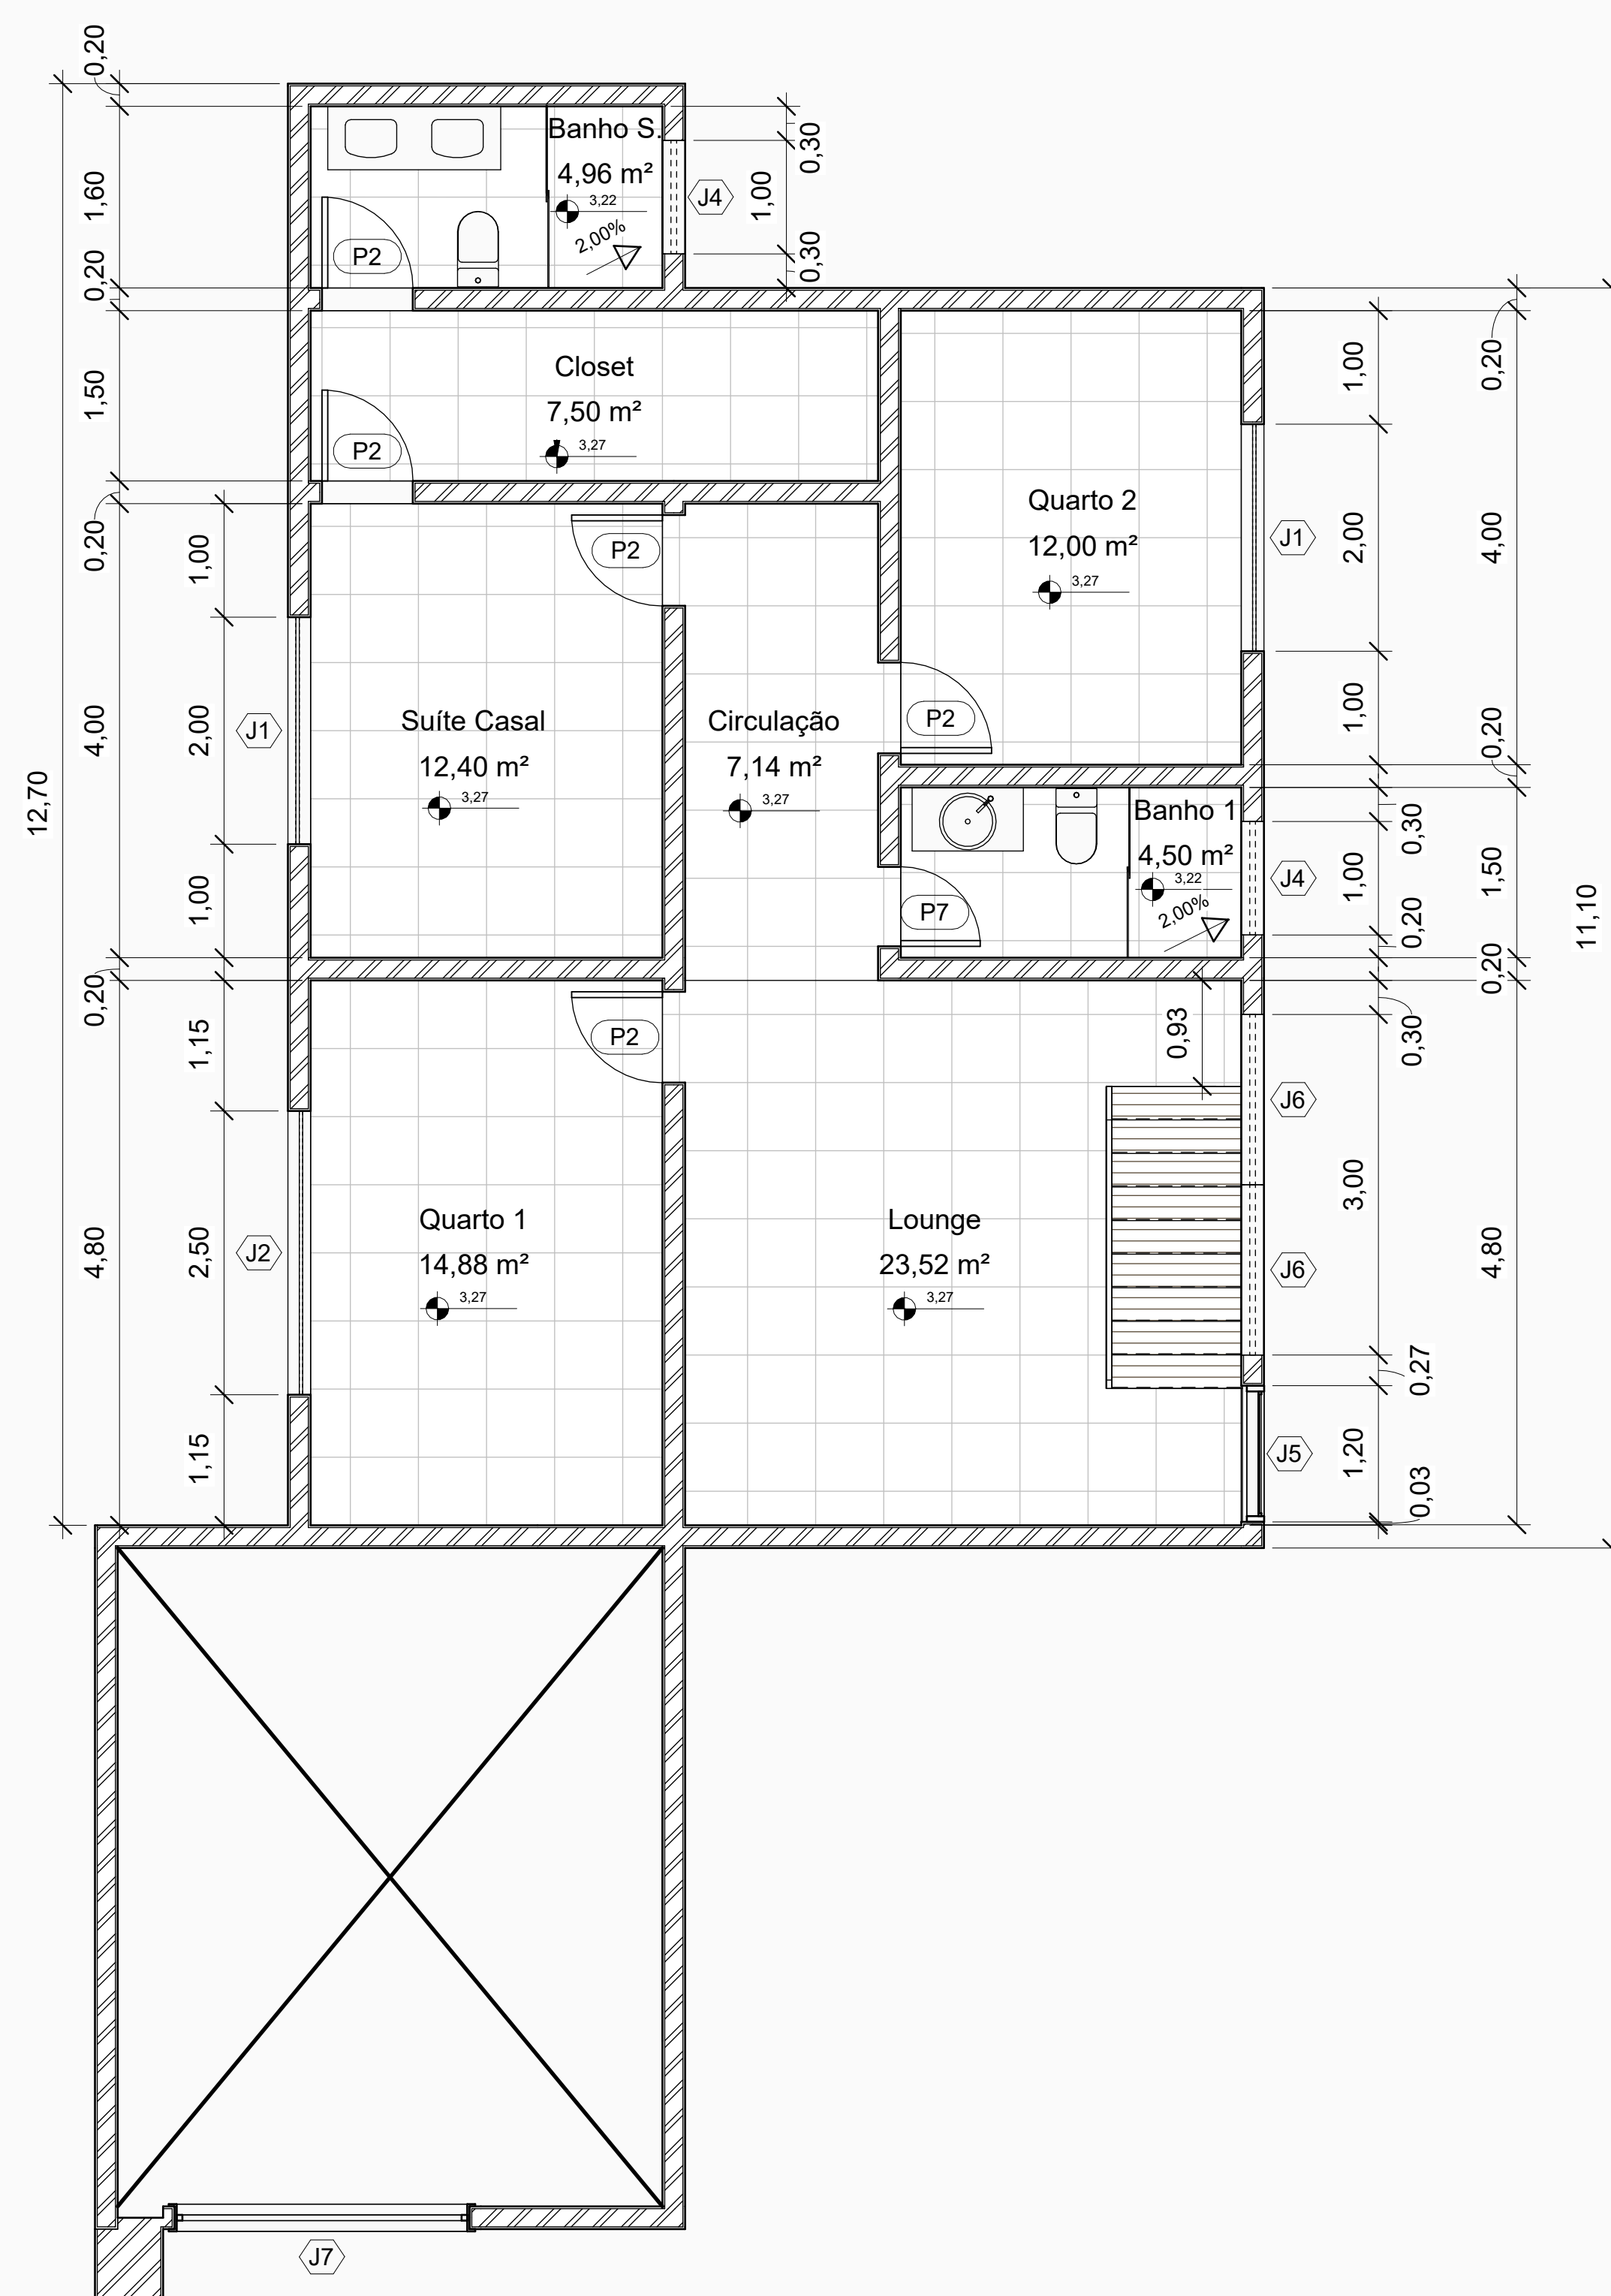


4 PLANTA BAIXA PAV.
SUPERIOR
1 : 50

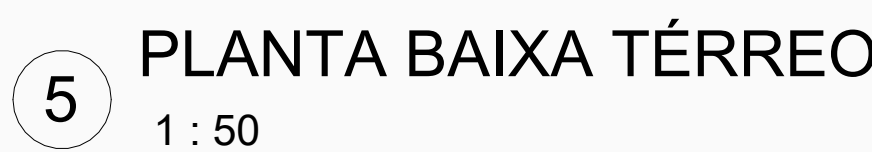


Quadro de Janelas			
Marca de tipo	Largura	Altura	Quant.
J1	2,00	1,20	4
J2	2,50	1,20	1
J3	1,00	0,40	3
J4	1,00	0,60	2
J5	1,20	4,00	1
J6	1,50	0,80	4
J7	2,60	5,70	1
J8	1,80	1,20	1

Quadro de Portas			
Marca de tipo	Largura	Altura	Quant.
P1	1,10	2,10	1
P2	0,80	2,10	6
P3	2,50	2,10	1
P4	1,40	2,10	1
P5	1,50	2,10	1
P7	0,70	2,10	5
P8	0,90	2,10	1


 CONSTRUTOR JÚNIOR		AV. DOUTOR SILVIO MENICUCCI, S/N, DEP. DE ENGENHARIA (DEG), CAMPUS DA UNIVERSIDADE FEDERAL DE LAVRAS, LAVRAS, MG. CNPJ: 28.098.875/0001-97 TEL.: (35) 4104-4102 EMAIL: contato@construjr.com.br	
PROJETO PARA CONSTRUÇÃO / REFORMA / REGULARIZAÇÃO / DEMOLIÇÃO		FOLHA:	A0
FINALIDADE: APROVAÇÃO INICIAL DE PROJETO USO RESIDENCIAL UNIFAMILIAR		Processo _____ / _____ FOLHA Nº ____ DE ____ FOLHAS	
LOCALIZAÇÃO DO LOTE: Município XX _____ QUILÔMETRO _____ LOTES _____		INSCRIÇÃO IMOBILIAR: _____ CADASTRO DO IMÓVEL _____ ZONA DE PROTEÇÃO _____ ZONAMENTO _____	
BAIRRO: _____		MUNICÍPIO: _____	
GOVERNO DE LAVRAS			
			
SECRETARIA DE OBRAS Subsecretaria de Regulação Urbana			
QUADRO DE ÁREAS			
TERRENO _____ m²		361,73 m²	
APROVAÇÃO TÉCNICA NOTIFICAÇÃO DE OBRA		REGULARIZAÇÃO DE OBRA	
ÁREA DE PROJEÇÃO: _____	201,10 m²	ÁREA EXISTENTE: _____	
ÁREA A CONSTRUIR: _____	329,56 m²	ÁREA ARBORIZADA: _____	
ÁREA ARBORIZADA: _____		ÁREA APROVADA: _____	
ÁREA ARBORIZADA: _____		ÁREA DE ACRESCIMTO: _____	
ÁREA TOTAL: _____		TOTAL A REGULARIZAR: _____	
_____	329,56 m²		
PERMEABILIDADE DO TERRENO			
ÁREA PERMEÁVEL _____	51,28m²	TAXA DE PERMEABILIZACÃO _____	14,18%
QUANDO USO MISTO			
ÁREA RESIDENCIAL _____		ÁREA NÃO RESIDENCIAL _____	
PAGAMENTOS E OCUPAÇÃO CASABERTO			
TAXA DE OCUPAÇÃO _____	54%	Nº DE UNIDADES _____	
UNIDADES RESIDENCIAIS _____		UNIDADES NÃO RESIDENCIAIS _____	
RESPONSÁVEL PELO PROCESSO: _____ CPF / CNPJ _____			
ASSINATURA DOS RESPONSÁVEIS PELO PROCESSO COORDENADORES DE PROCESSOS ANTERIORES, ETC)			
RESPONSÁVEL TÉCNICO PELA PROPOSTA RESPONSÁVEL TÉCNICO PELA PROPOSTA CREA - CAU - CPT / UF _____ CREA - CAU - CPT / UF _____			
ASSINATURA DO RESPONSÁVEL TÉCNICO PELA PROPOSTA			
Conferme La Complementar 425/2011 e sua alteração que dispõem sobre o Código de Obras do Município de Lavras, Minas Gerais, em seu dispositivo 1. Condições em termos de área mínima construída, número mínimo de plantas desenhadas, condições mínimas de estrutura e detalhes e extra informações da proposta que não são objeto de avaliação previstas no Art. 3º e suas alterações desta Lei Complementar. Conferir termo de compromisso assinado pelo município (polícia) juntamente representando Técnico(a) para assinar como a área(s) e permeabilidade está compatibilizada com relação aos demais regulamentos na ordem Municipal, Estadual e Federal.			
PROJETO APROVADO / APTO PARA VISTORIA Conferme La Complementar 425/2011 e sua alteração. Código de Obras e demais legislações pertinentes à este departamento.			

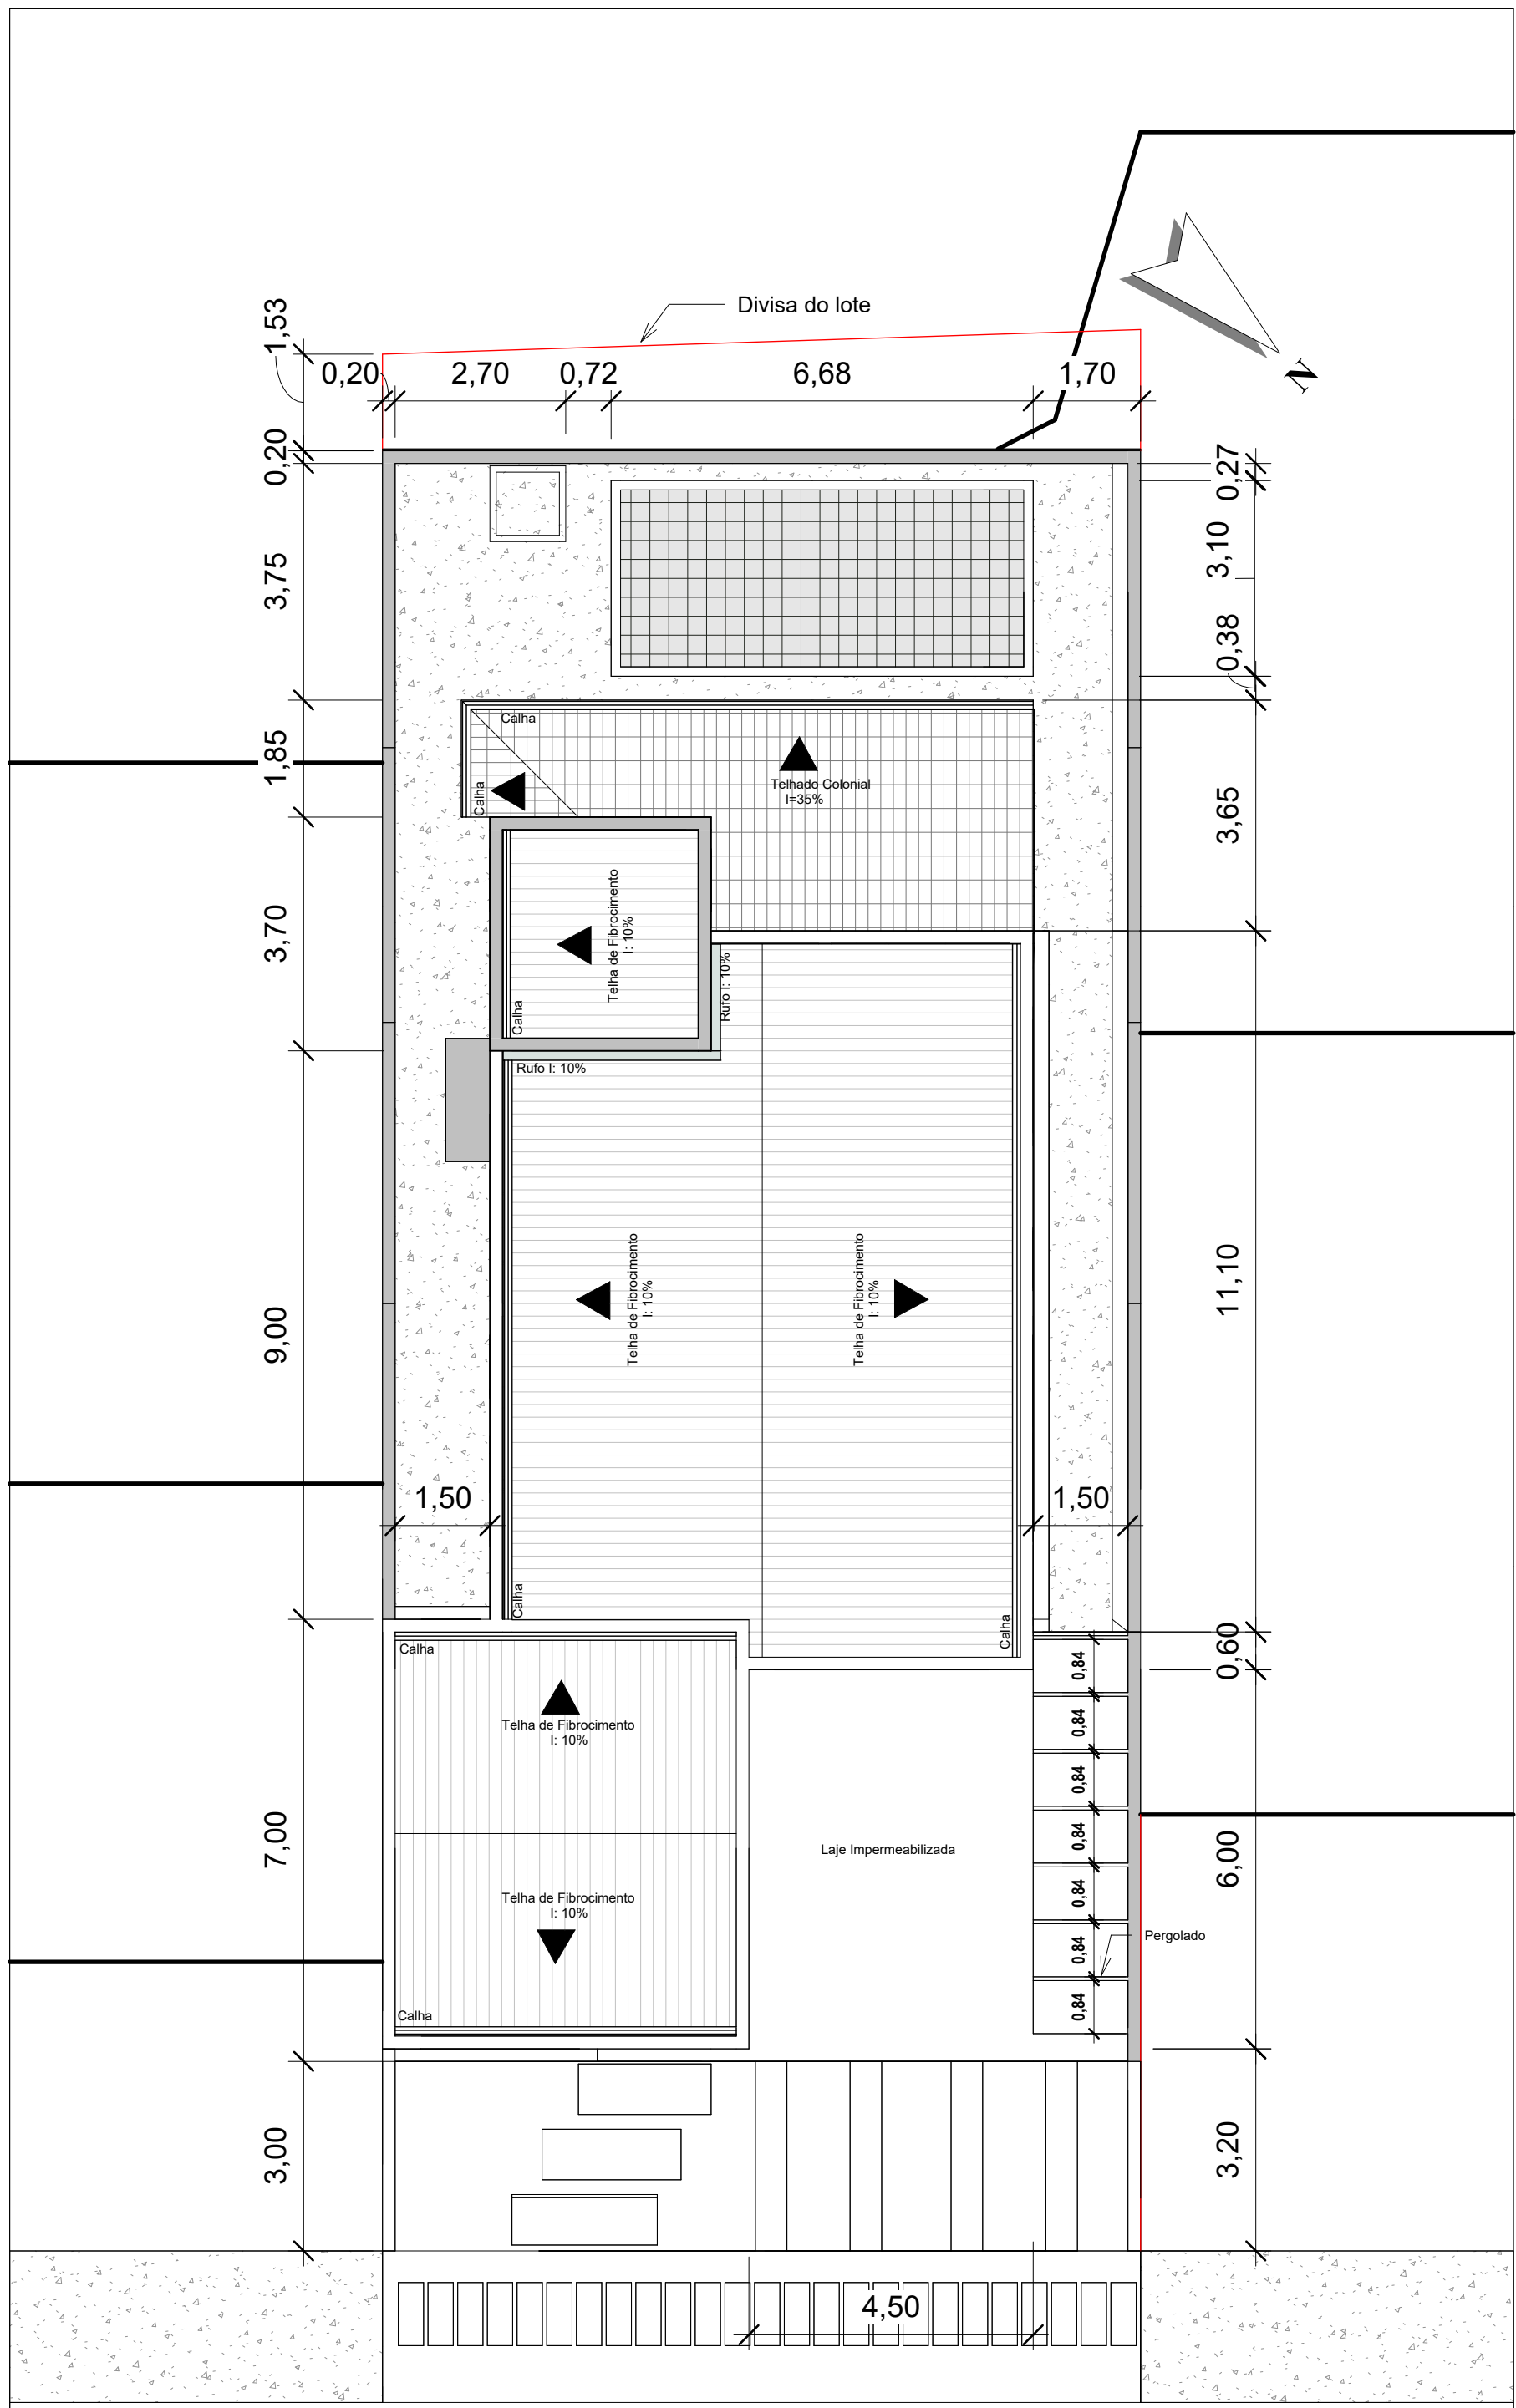


1 DIAGRAMA DE COBERTURA
1:100

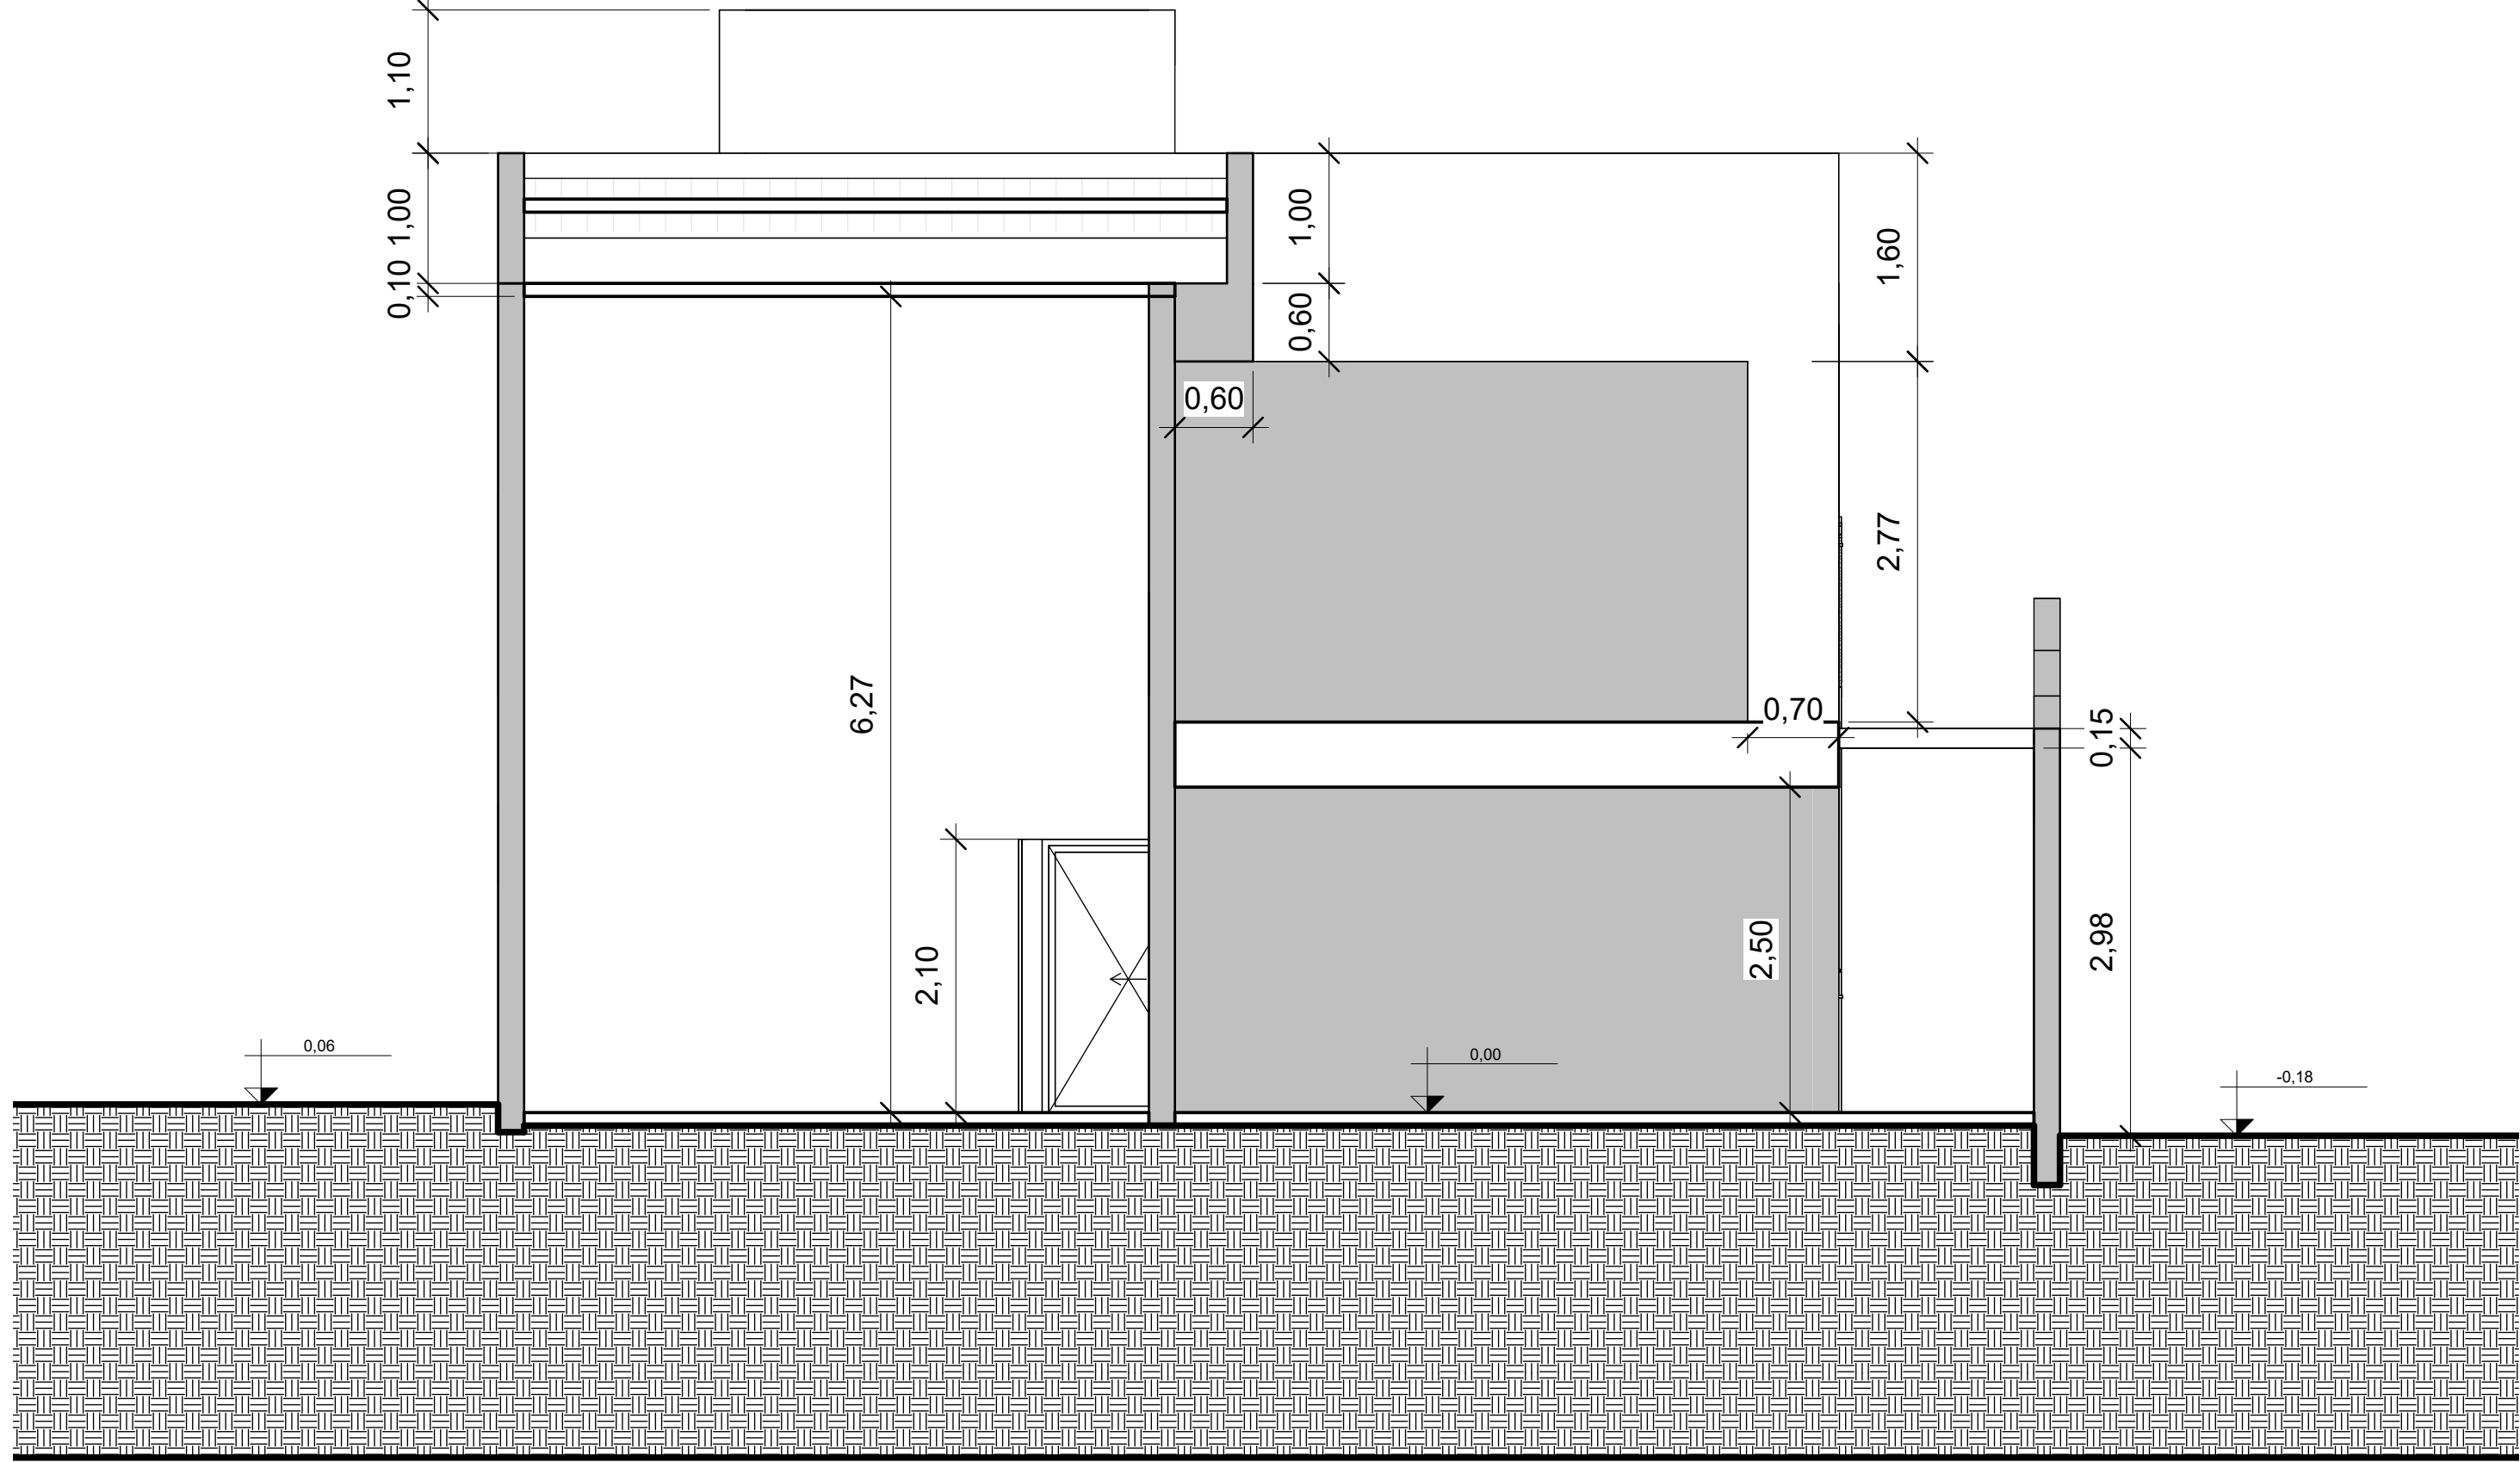

2 CORTE AA
1:50

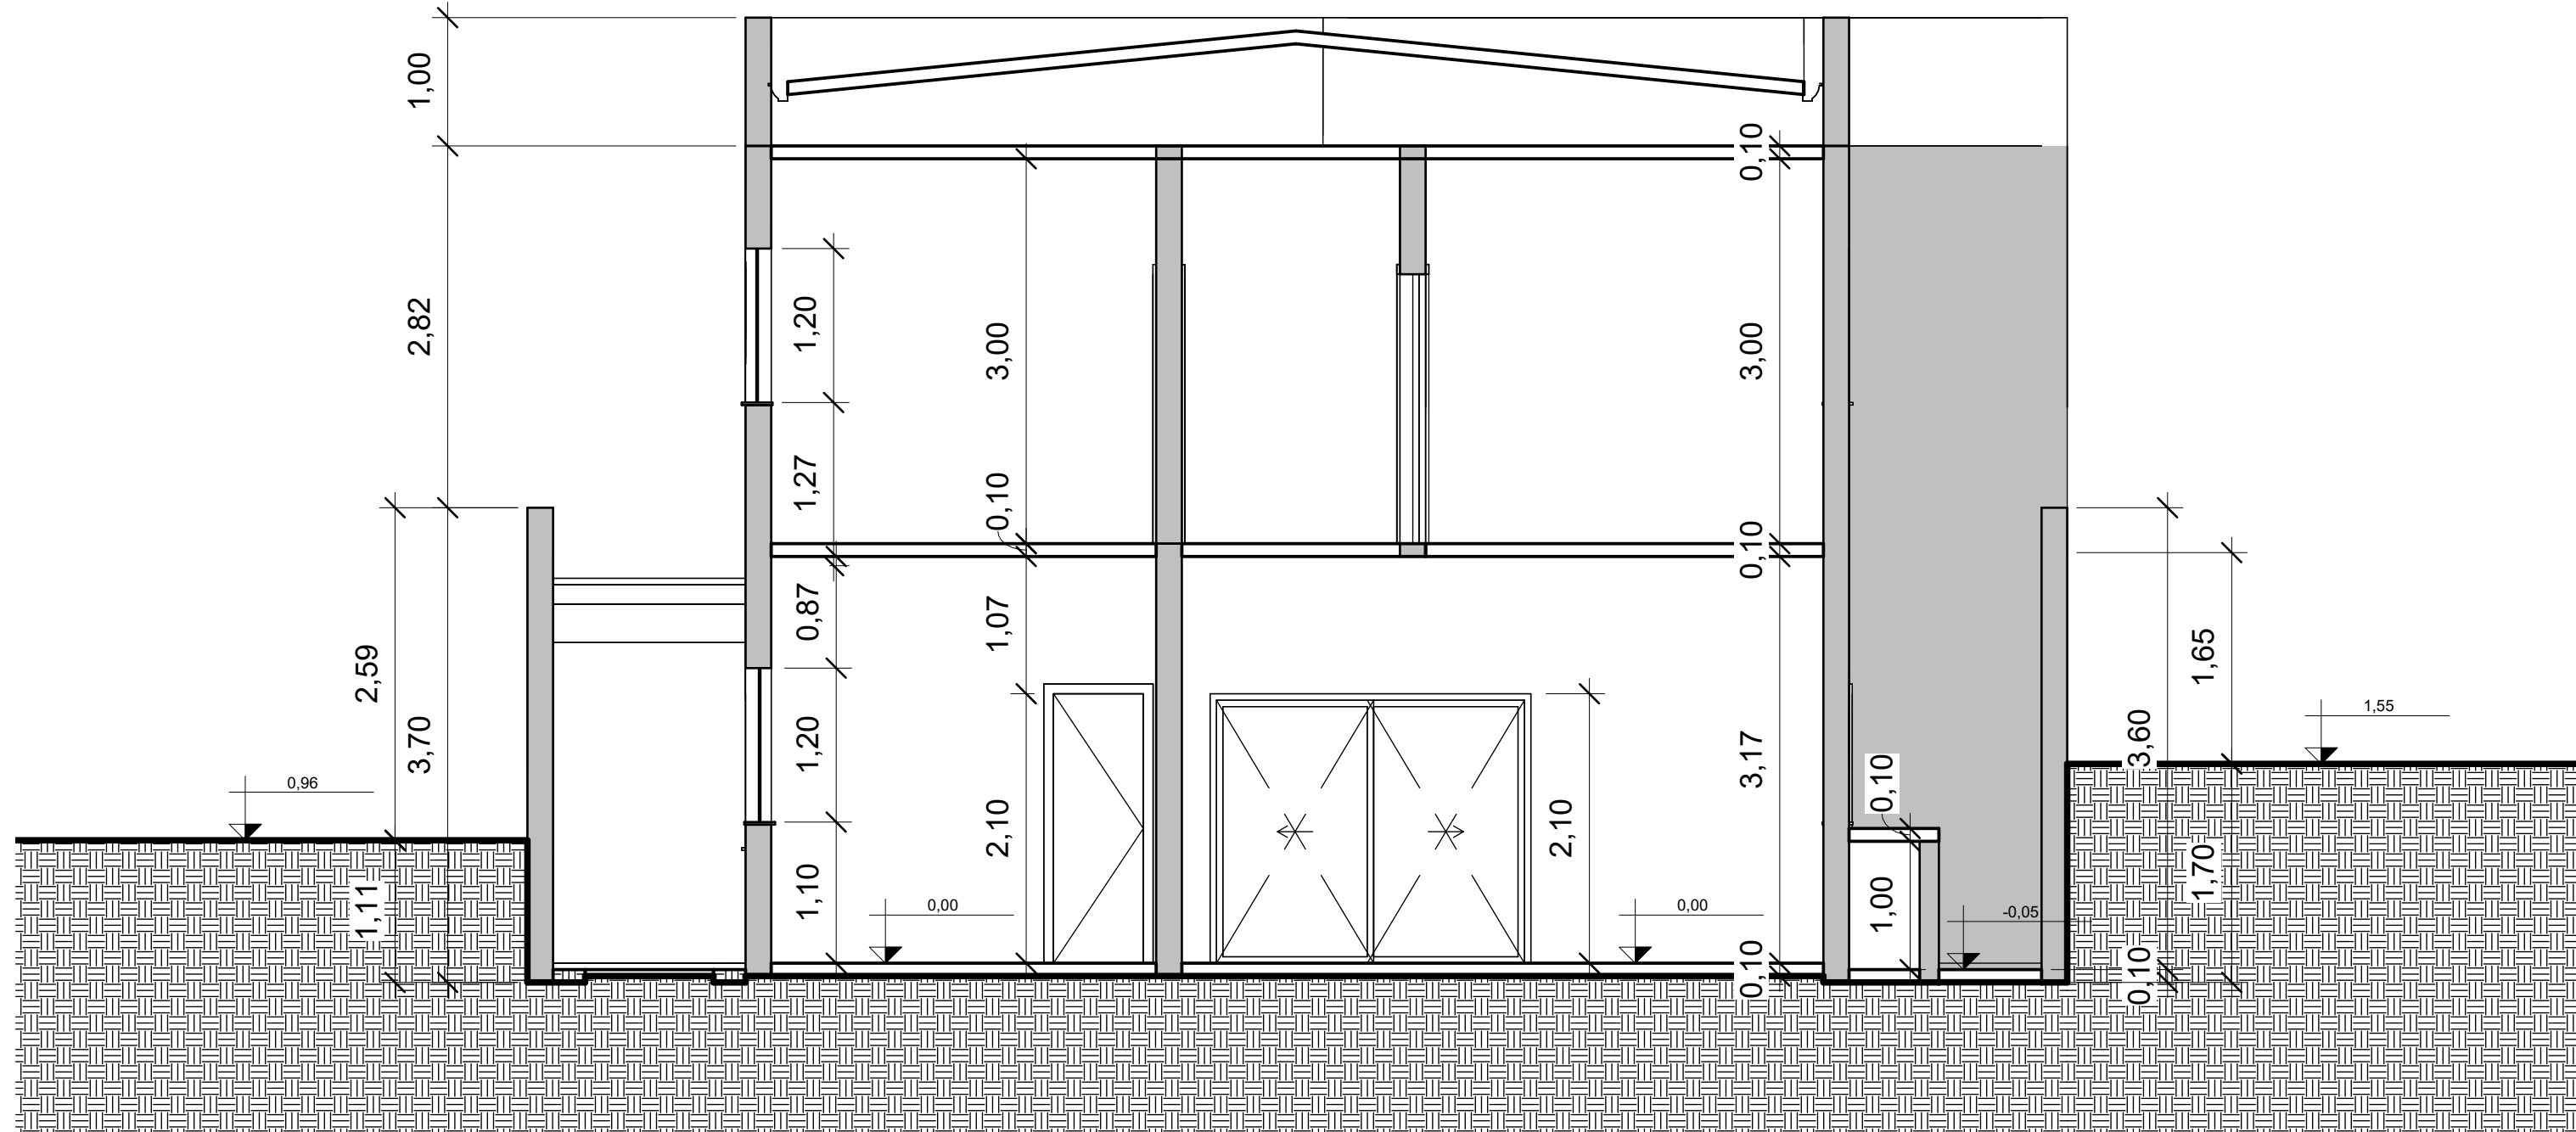

3 CORTE BB
1:50

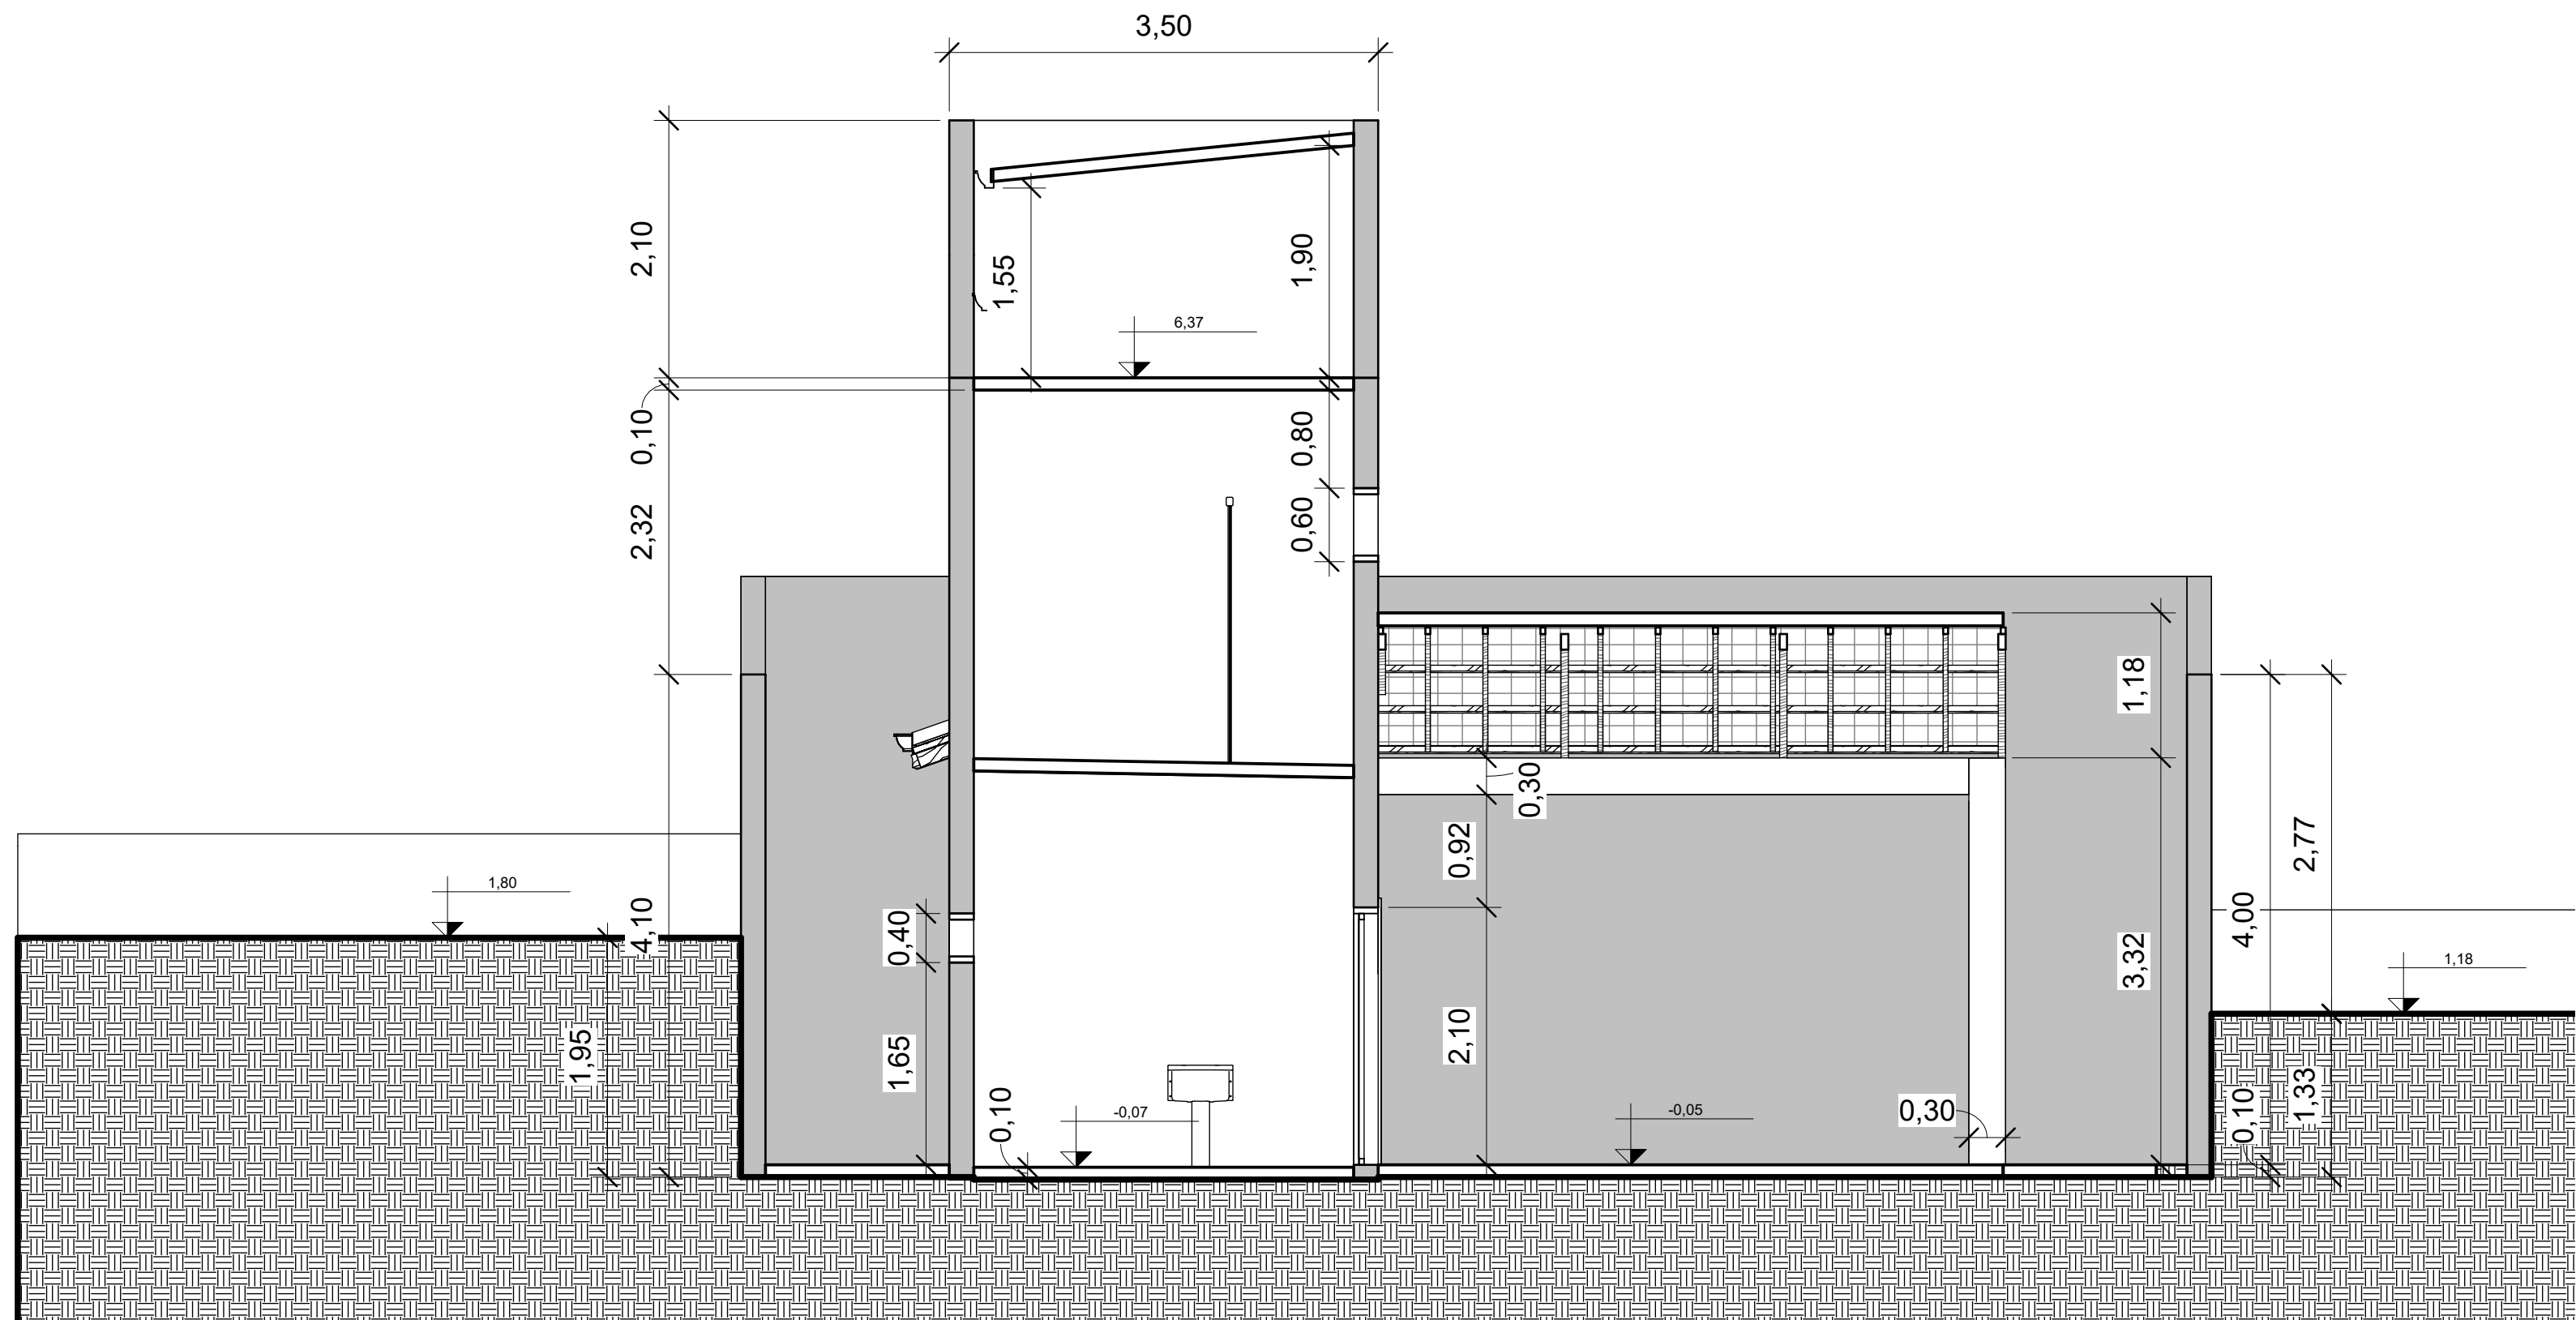

4 CORTE CC
1:50

		EMPRESA JÚNIOR DE ENGENHARIA CIVIL AV. DOUTOR SILVIO MENCIOCCI, S/N, DEP. DE ENGENHARIA (DEG), CAMPUS DA UNIVERSIDADE FEDERAL DE LAVRAS, LAVRAS, MG. CNPJ: 28.088.875/0001-97 TEL.: (35) 4104-4102 EMAIL: contato@construjr.com.br	
PROJETO PARA CONSTRUÇÃO / REFORMA / REGULARIZAÇÃO / DEMOLIÇÃO		FOLHA: A0	
USO: RESIDENCIAL UNIFAMILIAR		FOLHA Nº: ____ / RUBRICA: ____	
LOGRADOURO: [REDACTED]		INSCRIÇÃO PROFISSIONAL: [REDACTED]	
NÚMERO: XX QUADRA: [REDACTED] LOTE: [REDACTED]		CADASTRO DO IMÓVEL: [REDACTED]	
BAIRRO: [REDACTED] MUNICÍPIO: [REDACTED]		TOMAMENTO: [REDACTED] ZONEAMENTO: [REDACTED]	
GOVERNO DE LAVRAS  SECRETARIA DE OBRAS Subsecretaria de Regulação Urbana			
RESPONSÁVEL PELO PROCESSO: CPF / CNPJ: [REDACTED]			
ASSINATURA DO(S) RESPONSÁVEL(ES) PELO PROCESSO: [REDACTED]			
OBSERVAÇÕES (Nº DE PROCESSOS ANTERIORES, ETC):			
RESPONSÁVEL TÉCNICO PELO PROJETO: CPF / CNPJ: [REDACTED]			
ASSINATURA DO RESPONSÁVEL TÉCNICO PELO PROJETO: [REDACTED]			
Conferir o Lei Complementar 425/2021 e suas alterações que dispõem sobre o Código de Obras do município e demais legislações pertinentes a este empreendimento, a permissão de obras e a área de obra, bem como a responsabilidade técnica do projeto, bem como a emissão de licenças e a outorga de informações do projeto que não são objeto de avaliação, aprovação ou não, de aprovação ou não do empreendimento. Condições de regularização remissão do município para o município responsável. Responsabilidade pelo projeto cabe à (s) e a responsabilidade pela compatibilidade em relação aos dados reguladores nas esferas Municipal, Estadual e Federal.			
QUADRO DE ÁREAS TERRENO: 361,73 m²			
APROVAÇÃO INICIAL / NOTIFICAÇÃO DE PROJETO ÁREA DE PROJEÇÃO: 201,10 m² ÁREA A CONSTRUIR: 329,56 m² ÁREA APROVADA: [REDACTED] ÁREA AVERBADA: [REDACTED] ÁREA TOTAL: 329,56 m²		REGULARIZAÇÃO DE OBRA ÁREA EXISTENTE: [REDACTED] ÁREA AVERBADA: [REDACTED] ÁREA APROVADA: [REDACTED] ÁREA DE ACRESCIMENTO: [REDACTED] TOTAL A REGULARIZAR: [REDACTED]	
PERMEABILIDADE DO TERRENO ÁREA PERMEÁVEL: 51,28m² TAXA DE PERMEABILIDADE: 14,18%			
QUANDO USO MISTO ÁREA RESIDENCIAL: [REDACTED] ÁREA NÃO RESIDENCIAL: [REDACTED]			
PAVIMENTOS E OCUPAÇÃO GARAGEM: [REDACTED] TOTAL DE PAVIMENTOS: 2 TAXA DE OCUPAÇÃO: 54% Nº DE UNIDADES: [REDACTED] UNIDADES RESIDENCIAIS: [REDACTED] UNIDADES NÃO RESIDENCIAIS: [REDACTED]			
PROJETO APROVADO / APTO PARA VISTORIA Código de Obras e demais legislações pertinentes a este empreendimento.			





EMPRESA JÚNIOR DE ENGENHARIA CIVIL
 AV. DOUUTOR SÍLVO MENIGUICCI, S/N, DEP. DE ENGENHARIA (DEG),
 CAMPUS DA UNIVERSIDADE FEDERAL DE LAVRAS, LAVRAS, MG
 CNPJ: 26.086.875/0001-67
 TEL.: (35) 4104-4102 EMAIL: contato@construi.com.br

PROJETO PARA CONSTRUÇÃO / REFORMA / REGULARIZAÇÃO / DEMOLIÇÃO	FOLHA: A0
--	-------------------------

FINALIDADE: APROVAÇÃO INICIAL DE PROJETO USO: RESIDENCIAL UNIFAMILIAR	PROCESSO _____ / _____ FOLHA Nº _____ DE _____ FOLHAS
LOGOADOIRO: _____ NOME: _____ QUADRO: _____ LOT: _____ DISTRITO: _____	INSCRIÇÃO (PROFISSIONAL): _____ CAIXOTE DO PRÓJETO: _____ ZONA/SETOR: _____ ZONA/SETOR: _____

MUNICÍPIO: LAVRAS - MG

GOVERNO DE LAVRAS



SECRETARIA DE OBRAS

Subsecretaria de Regulação Urbana

RESPONSÁVEL PELO PROCESSO: _____

CNPJ / CDT: _____

ASSINATURA DO(S) RESPONSÁVEL(ES) PELO PROCESSO

OBSERVAÇÕES (SE Houver PROCESSOS ANTERIORES, ETC)

QUADRO DE ÁREAS
 TERRENO: _____ 361,73 m²

APROVAÇÃO INICIAL MODIFICAÇÃO DE PROJETO	REGULARIZAÇÃO DE OBRA
ÁREA DE PROJEÇÃO: 201,10 m²	ÁREA EXISTENTE: _____
ÁREA A CONSTRUIR: 329,56 m²	ÁREA AVERBADA: _____
ÁREA APROVADA: _____	ÁREA APROVADA: _____
ÁREA AVERBADA: _____	ÁREA DE ACRESCIMO: _____
ÁREA TOTAL: 329,56 m²	TOTAL A REGULARIZAR: _____

PERMABILIDADE DO TERRENO	TAXA DE PERMABILIDADE
ÁREA PERMÉVEL: 51,28m²	14,18%

QUANDO USO MISTO

ÁREA RESIDENCIAL	ÁREA NÃO RESIDENCIAL
------------------	----------------------

PAVIMENTOS E OCUPAÇÃO GABARITO	TOTAL DE PAVIMENTOS
TAXA DE OCUPAÇÃO: 54%	Nº DE UNIDADES: _____
UNIDADES RESIDENCIAIS	UNIDADES NÃO RESIDENCIAIS

RESPONSÁVEL TÉCNICO PELO PROCESSO: _____




RESPONSÁVEL TÉCNICO PELO PROJETO
 OBRA - CAU - CRT / UF
 CREA - CAU - CRT / UF

ASSINATURA DO RESPONSÁVEL TÉCNICO PELO PROJETO

Conferme! Na Complementar 452/2012 e suas alterações que dispõem sobre o Código de Obras do município e demais legislações pertinentes e não o departamento, e portanto não reenvia o projeto de análise as dependências internas do projeto, direcionados de imediato, visto que direciona a outra interdependência do projeto que não são dentro do município, porém a responsabilidade do município possui eventual responsabilidade Técnico(a) pelo projeto e não a responsabilidade por compatibilidade em relação aos demais órgãos responsáveis nas esferas Municipal, Estadual e Federal.

PROJETO APROVADO / APTO PARA VISTORIA

Conferme! Na Complementar 452/2012 e suas alterações,
 Código de Obras e demais legislações pertinentes a este departamento.

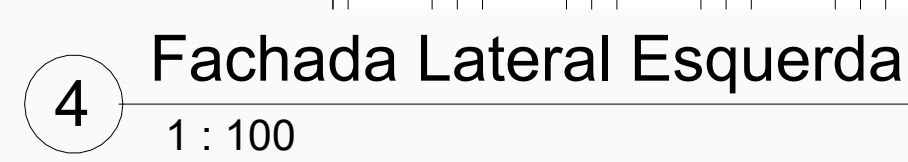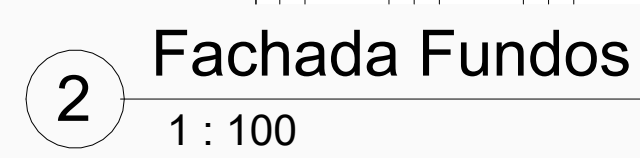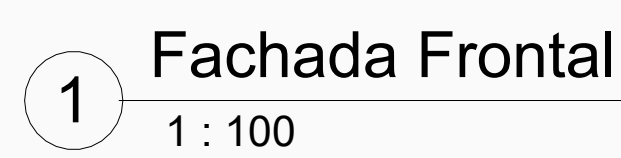

		EMPRESA JÚNIOR DE ENGENHARIA CIVIL	
AV. DOUÇOUR SILVIO MENEGUCCI, S/N, DEP. DE ENGENHARIA (DEG), CAMPUS DA UNIVERSIDADE FEDERAL DE LAVRAS (UFEL), CNPJ: 26.088.975/0001-97 TEL.: (35) 4104-4102 EMAIL: contato@construm.br			
PROJETO PARA CONSTRUÇÃO / REFORMA / REGULARIZAÇÃO / DEMOLIÇÃO		FOLHA:	A0
FINALIDADE: APROVAÇÃO INICIAL DE PROJETO USO: RESIDENCIAL UNIFAMILIAR		PONTO N° _____ / _____ _____, ____ DE _____, _____	
LUGAR/OBRAS: [REDACTED] NOME: XX QUADRO: [] LOTE: [] BAIRRO: [REDACTED] MUNICÍPIO: [REDACTED]		INSCRIÇÃO PROFISSIONAL: [REDACTED] GABINETE DO PROJET. [REDACTED]	ZONAAMENTO: ZONATEMTO
GOVERNO DE LAVRAS SECRETARIA DE OBRAS Subsecretaria de Regulação Urbana		RESPONSÁVEL PELO PROCESSO: [REDACTED] CPF / CDT: [REDACTED] ASSINATURA DO RESPONSÁVEL PELO PROCESSO: [REDACTED] OBSERVAÇÕES DE PRÉ-PROCESSOS ANTERIORES, ETC)	
QUADRO DE ÁREAS			
TERRENO 361,73 m²			
APROVAÇÃO INICIAL REGULATÓRIA DE PROJETO		REGULARIZAÇÃO DE OBRA	
ÁREA DE PRODUÇÃO: 201,10 m²	ÁREA EXISTENTE:		
ÁREA A CONSTRUIR: 329,56 m²	ÁREA ARBORIZADA:		
ÁREA APROVADA:	ÁREA APROVADA:		
ÁREA AVERBUADA:	ÁREA DE ACRESCHIMO:		
ÁREA TOTAL: 329,56 m²	TOTAL A REGULARIZAR:		
PERMEABILIDADE DO TERRENO			
ÁREA PERMEÁVEL: 51,28m²	TAXA DE PERMEABILIDADE: 14,18%		
QUANDO USO MISTO			
ÁREA RESIDENCIAL	ÁREA NÃO RESIDENCIAL		
PAGAMENTOS E OCUPAÇÃO			
GABARITO	TOTAL DE PAGAMENTOS		
	2		
TAXA DE OCUPAÇÃO	Nº DE UNIDADES		
54%			
UNIDADES RESIDENCIAIS	UNIDADES NÃO RESIDENCIAIS		
PROJETO APROVADO / APTO PARA VISTORIA Conferir as seguintes observações pertinentes à este documento.			