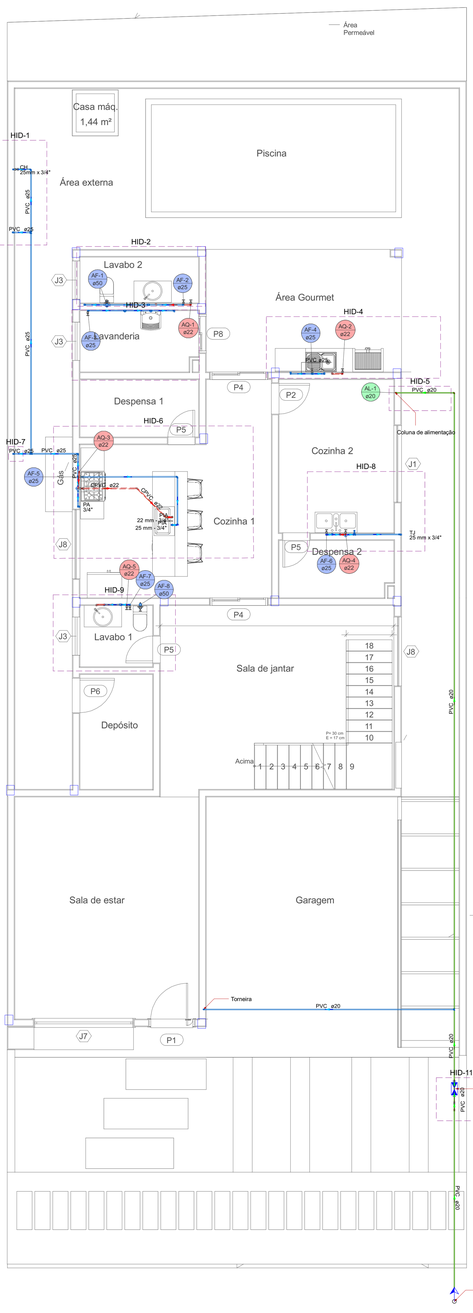

Lista de materiais - Térreo		
Alimentação		
	Ferro maleável classe 10	
	Bujão	
	1/2"	1 pç
	Contraporca	
	1/2"	1 pç
	Cotovelo 90	
	1/2"	3 pç
	Luva	
	1/2"	2 pç
	Tubo de aço galvanizado	
	15 mm - 1/2"	1 m
	Tê	
	1/2"	1 pç
Metais		
	Registro de Pressão DOCOL JET 30	
	1/2"	1 pç
	Registro de esfera	
	1/2"	1 pç
	Válvula de Esfera	
	1/2"	1 pç
PVC misto soldável		
	Colar de tomada em PVC	
	1/2"	1 pç
	Joelho 90 soldável c/ rosca	
	20 mm - 1/2"	1 pç
PVC rígido soldável		
	Adapt sold.curto c/bolsa-rosca p registro	
	20 mm - 1/2"	3 pç
	Joelho 90º soldável	
	20 mm	6 pç
	Luva soldável	
	20 mm	1 pç
	Tubos	
	20 mm	28.63 m
Água fria		
	Aparelho	
	Chuveiro	
	25mm x 3/4"	1 pç
	Ducha higiênica	
	25mm x 1/2"	2 pç
	Máquina de Lavar Roupa	
	25mm x 3/4"	1 pç
	Purificador de água	
	3/4"	3 pç
	Torneira de Jardim	
	20mm x 1/2"	1 pç
	25 mm x 3/4"	2 pç
	Torneira de Pia de Cozinha	
	25mm - 3/4"	3 pç
	Torneira de Tanque de Lavar	
	25mmx 3/4"	3 pç
	Torneira de lavatório	
	25 mm - 1/2"	2 pç
	Vaso Sanitário p/ Válvula de Descarga de 1 1/2"	
	40mm - 1 1/2"	2 pç
Metais		
	Registro Globo	
	1.1/2"	1 pç
	Registro de gaveta c/ canopla cromada	
	1.1/2"	1 pç
	3/4"	7 pç
	Válvula de descarga baixa pressão	
	1.1/2"	2 pç
PVC Acessórios		
	Bolsa de ligação p/ vaso sanitário	
	1.1/2"	2 pç
	Engate flexível plástico	
	1/2 - 30cm	2 pç
	Tubo de descarga VDE.	
	38 mm	2 pç
	Tubo de ligação latão cromado c/ canopla p/ vaso Sa.	
	38 mm	2 pç
PVC rígido soldável		
	Adapt sold.curto c/bolsa-rosca p registro	
	25 mm - 3/4"	14 pç
	50 mm - 1.1/2"	6 pç
	Curva de transposição	
	25 mm	3 pç
	Joelho 90º soldável	
	20 mm	1 pç
	25 mm	20 pç
	Luva de correr p/ tubo	
	25 mm	3 pç
	50 mm	2 pç
	Luva soldável	
	25 mm	3 pç
	Tubos	
	20 mm	6.78 m
	25 mm	45.72 m
	50 mm	2.17 m
	Tê 90 soldável	
	20 mm	1 pç
	25 mm	10 pç
PVC soldável anel c/ bucha latão		
	Joelho 90º soldável com bucha de latão	
	20 mm - 1/2"	1 pç
	25 mm - 3/4"	13 pç
	Joelho de redução 90º soldável com bucha de latão	
	25 mm- 1/2"	4 pç
Água quente		
	CPVC Aquatherm	
	Conector	
	22 x 3/4"	10 pç
	Joelho 45	
	22 mm	2 pç
	Joelho 90	
	22 mm	12 pç
	Joelho 90º de transição	
	22 x 1/2"	2 pç
	22 x 3/4"	2 pç
	Luva	
	22 mm	4 pç
	Luva de correr	
	22 mm	1 pç
	Tubo CPVC 3 Mts	
	22 mm	19.4 m
	Tê de transição	
	22 x 3/4"	1 pç
Metais		
	Registro de gaveta c/ canopla cromada	
	3/4"	5 pç
PVC Acessórios		
	Engate flexível cobre cromado com canopla	
	1/2 - 30cm	2 pç

Legenda de condutos - Térreo
Água fria
Água quente
Alimentação

Legenda - Térreo
Alimentador Predial
Curva de transposição
Hidrômetros
Registro de gaveta c/canopla cromada c/ CPVC
Registro de gaveta c/canopla cromada c/PVC soldável
Registro globo c/ PVC soldável
Válvula de descarga c/PVC soldável
Válvula de esfera c/ PVC soldável

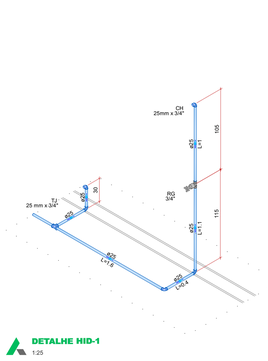

DETALHE HID-1
1:25

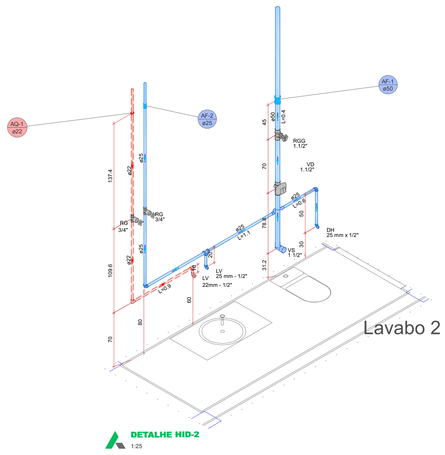

DETALHE HID-2
1:25

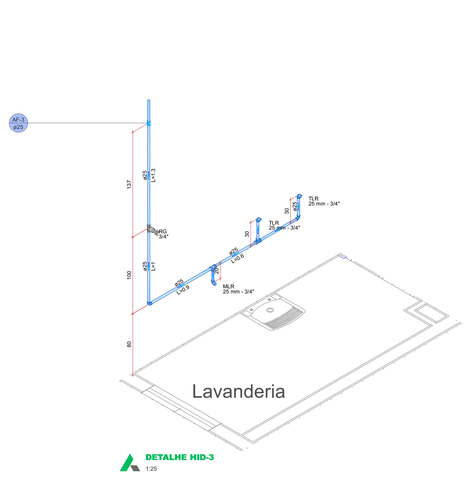

DETALHE HID-3
1:25

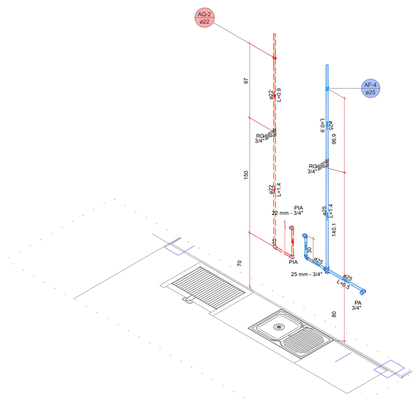

DETALHE HID-4
1:25

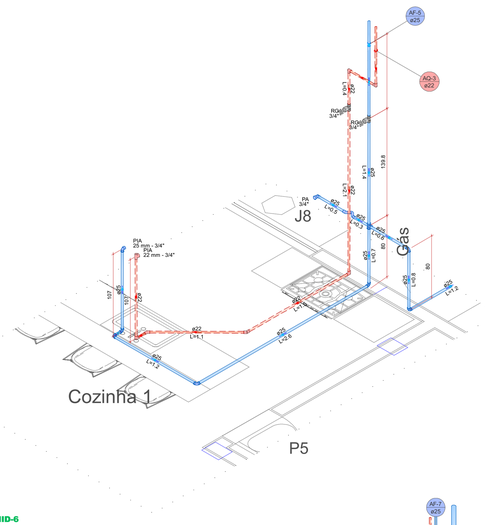

DETALHE HID-6
1:25

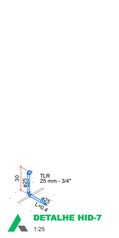

DETALHE HID-7
1:25

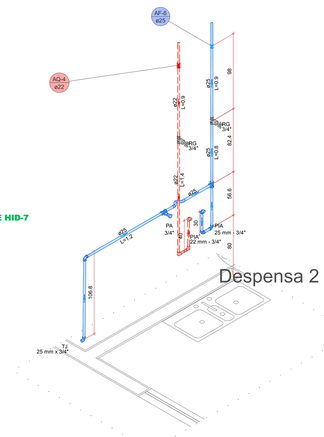

DETALHE HID-8
1:25

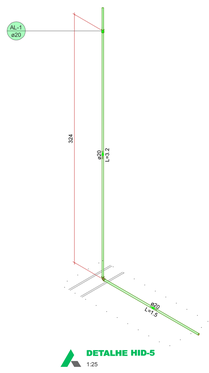

DETALHE HID-5
1:25

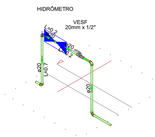

DETALHE HID-11
1:25

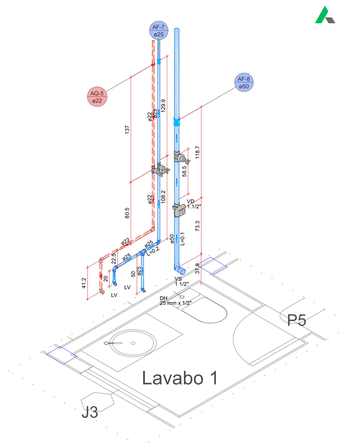

DETALHE HID-9
1:25

CONSTRU JÚNIOR	EMPRESA JÚNIOR DE ENGENHARIA CIVIL AV. DOUTOR SILVIO MENICUCCI, S/N, DEP. DE ENGENHARIA (DEG), CAMPUS DA UNIVERSIDADE FEDERAL DE LAVRAS, LAVRAS, MG CNPJ: 28.098.973/0001-97, TEL.: (35) 4104-4102 - EMAIL: contato@construjr.com.br
TÍTULO:	PROJETO HIDROSSANITÁRIO RESIDÊNCIAL
CONTEÚDO:	HIDROSSANITÁRIO
LOCALIZAÇÃO: [redacted]	ESCALA: 1/50
CLIENTE: [redacted]	OPERADOR: [redacted] DATA: 13/05/25
RESPONSÁVEL TÉCNICO: [redacted]	CREA: [redacted] FOLHA: 01/

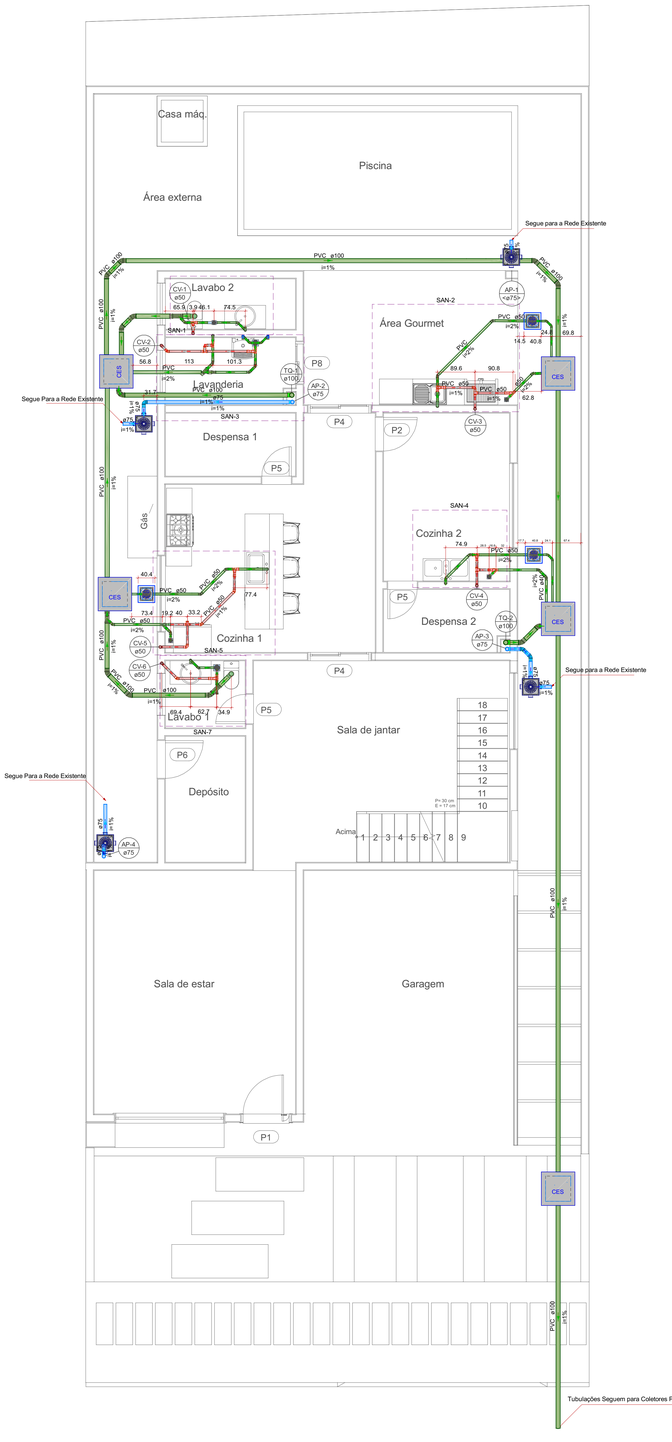

Legenda detalhada - Térreo	
Caixa Sifonada	
PVC Acessórios	
Caixa sifonada	
100x100x50	1pç
PVC Esgoto	
Anel de borracha	
50mm - 2"	1pç
Caixa de areia pluvial PVC	
Caixas de Passagem	
Caixa de areia pluvial PVC	
CA PVC - 30 cm	1pç
Caixas Inspeção Esgoto Sifonada	
Caixas de Passagem	
Caixa de inspeção de esgoto sifonada	
CES- 60x60 cm	1pç
Caixas de Gordura	
Caixas de Passagem	
Caixa de gordura PVC	
CG 30 cm	1pç
Joelho 45	
PVC Esgoto	
Anel de borracha	
50mm - 2"	1pç
Joelho 45	
50 mm	1pç
Joelho 90	
PVC Esgoto	
Anel de borracha	
50mm - 2"	1pç
Joelho 90	
50 mm	1pç
Joelho 90- coluna	
PVC Esgoto	
Anel de borracha	
100mm - 4"	1pç
75mm - 3"	1pç
Joelho 90	
100 mm	1pç
Redução excêntrica	
100 mm - 75 mm	1pç
Joelho 90- coluna bolsa	
PVC Esgoto	
Anel de borracha	
50mm - 2"	1pç
Joelho 90	
50 mm	1pç
Joelho 90- coluna sobe	
PVC Esgoto	
Anel de borracha	
75mm - 3"	1pç
Joelho 90	
75 mm	1pç
Junção invertida	
PVC Esgoto	
Anel de borracha	
100mm - 4"	1pç
50mm - 2"	1pç
Junção invertida	
100 mm x 50 mm	1pç
Junção simples	
PVC Esgoto	
Anel de borracha	
50mm - 2"	1pç
75mm - 3"	1pç
Junção simples	
75 mm - 50 mm	1pç
Lavatório. Residencial com sifão	
PVC Acessórios	
Sifão de copo p/ pia e lavatório	
1" - 1.1/2"	1pç
Válvula p/ lavatório e tanque	
1"	1pç
PVC Esgoto	
Curva 90 curta	
40 mm	1pç
Joelho 90 c/anel p/ esgoto secundário	
40 mm - 1.1/2"	1pç
Tubo rígido c/ ponta lisa	
40 mm	0.6m
Máquina de Lavar Roupas DN 50mm	
PVC Esgoto	
Anel de borracha	
50mm - 2"	2pç
Joelho 90	
50 mm	2pç
Tubo rígido c/ ponta lisa	
50 mm - 2"	0.9m
Pia de Cozinha Residencial com Sifão 50mm	
PVC Acessórios	
Sifão de copo p/ pia e lavatório	
1" - 2"	1pç
Válvula p/ pia	
1"	1pç
PVC Esgoto	
Anel de borracha	
50mm - 2"	2pç
Joelho 90	
50 mm	2pç
Tubo rígido c/ ponta lisa	
50 mm - 2"	0.6m
Ramais de Ventilação	
PVC Esgoto	
Anel de borracha	
50mm - 2"	3pç
Joelho 90	
50 mm	1pç
Tê sanitário	
50 mm - 50 mm	1pç
Redução excêntrica	
PVC Esgoto	
Anel de borracha	
50mm - 2"	1pç
Redução excêntrica	
75 mm - 50 mm	1pç
Tanque de Lavar Roupas DN 40mm	
PVC Acessórios	
Sifão flexível c/ Adaptador	
1.1/2" - 1.1/2"	1pç
Válvula p/ tanque	
1 1/2"	1pç
PVC Esgoto	
Curva 90 curta	
40 mm	1pç
Joelho 90 c/anel p/ esgoto secundário	
40 mm - 1.1/2"	1pç
Tubo rígido c/ ponta lisa	
40 mm	0.6m
Tê sanitário	
PVC Esgoto	
Anel de borracha	
50mm - 2"	2pç
Tê sanitário	
50 mm - 50 mm	1pç
Vaso Sanitário c/ J.90°	
PVC Esgoto	
Anel de borracha	
100mm - 4"	1pç
Joelho 90	
100 mm	1pç
Vedação p/ saída de vaso sanitário	
100 mm	1pç
Vaso Sanitário c/ curva 90°	
PVC Esgoto	
Anel de borracha	
100mm - 4"	1pç
Curva 90 curta	
100 mm	1pç
Vedação p/ saída de vaso sanitário	
100 mm	1pç

Lista de materiais - Térreo	
Esgoto	
Caixas de Passagem	
Caixa de gordura PVC	
CG 30 cm	3 pç
Caixa de inspeção de esgoto sifonada	
CES- 60x60 cm	5 pç
PVC Acessórios	
Caixa sifonada	
100x100x50	4 pç
150x150x50	2 pç
Sifão de copo p/ pia e lavatório	
1" - 1.1/2"	2 pç
1" - 2"	1 pç
Sifão flexível c/ Adaptador	
1.1/2" - 1.1/2"	2 pç
Válvula p/ lavatório e tanque	
1"	2 pç
Válvula p/ pia	
1"	1 pç
Válvula p/ tanque	
1.1/2"	2 pç
PVC Esgoto	
Anel de borracha	
100mm - 4"	20 pç
50mm - 2"	37 pç
75mm - 3"	1 pç
Curva 90 curta	
100 mm	1 pç
40 mm	4 pç
Joelho 45	
100 mm	13 pç
40 mm	8 pç
50 mm	15 pç
Joelho 90	
100 mm	3 pç
50 mm	9 pç
Joelho 90 c/anel p/ esgoto secundário	
40 mm - 1.1/2"	4 pç
Junção invertida	
100 mm x 50 mm	3 pç
Junção simples	
75 mm - 50 mm	1 pç
Luva simples	
50 mm	1 pç
Redução excêntrica	
75 mm - 50 mm	1 pç
Tubo rígido c/ ponta lisa	
100 mm - 4"	53.46 m
40 mm	8.4 m
50 mm - 2"	18.9 m
75 mm - 3"	1.66 m
Tê sanitário	
50 mm - 50 mm	1 pç
Vedação p/ saída de vaso sanitário	
100 mm	2 pç
Pluvial	
Caixas de Passagem	
Caixa de areia pluvial PVC	
CA PVC - 30 cm	4 pç
Condutor pluvial	
Circular metálico	
75 mm	7.62 m
PVC Esgoto	
Anel de borracha	
100mm - 4"	1 pç
75mm - 3"	6 pç
Joelho 45	
75 mm	2 pç
Joelho 90	
100 mm	1 pç
75 mm	3 pç
Redução excêntrica	
100 mm - 75 mm	1 pç
Ventilação	
PVC Esgoto	
Anel de borracha	
50mm - 2"	48 pç
Joelho 45	
50 mm	4 pç
Joelho 90	
50 mm	18 pç
Tubo PVC ponta-bolsa c/ virola	
50 mm - 2"	0.03 m
Tubo rígido c/ ponta lisa	
50 mm - 2"	10.18 m
Tê sanitário	
50 mm - 50 mm	13 pç

Legenda de condutos - Térreo
Esgoto
Pluvial
Ventilação

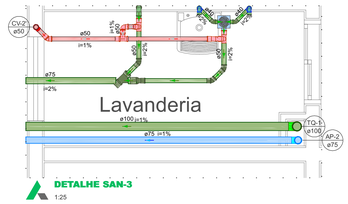

DETALHE SAN-3
1:25

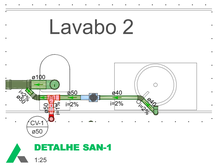

DETALHE SAN-1
1:25

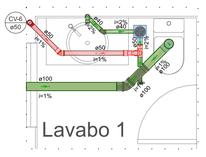

DETALHE SAN-7
1:25

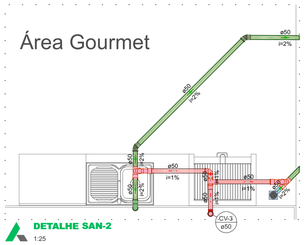

DETALHE SAN-2
1:25

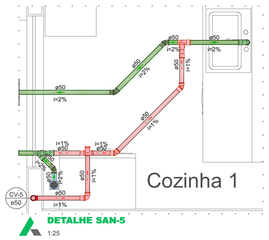

DETALHE SAN-5
1:25

DETALHE SAN-4
1:25

OBSERVAÇÃO:TUBULAÇÕES DESVIANDO DAS VIGAS BALDRAMES

CONSTRU JÚNIOR

EMPRESA JÚNIOR DE ENGENHARIA CIVIL
Av. DOUTOR SÍLVIO MENICUCCI, S/N, DEP. DE ENGENHARIA (DEG),
CAMPUS DA UNIVERSIDADE FEDERAL DE LAVRAS, LAVRAS, MG.
CNPJ: 28.098.875/0001-97 TEL.: (35) 4104-4102 EMAIL: contato@construjr.com.br

TÍTULO:	PROJETO HIDROSSANITÁRIO RESIDÊNCIAL		
CONTEÚDO:	HIDROSSANITÁRIO		
LOGRADOURO:	[redacted]	ESCALA:	1/50
CLIENTE:	[redacted]	OFICIO/Nº:	[redacted]
		DATA:	13/05/25
RESPONSÁVEL TÉCNICO:	[redacted]	OBRA:	[redacted]
		FOLHA:	01/03

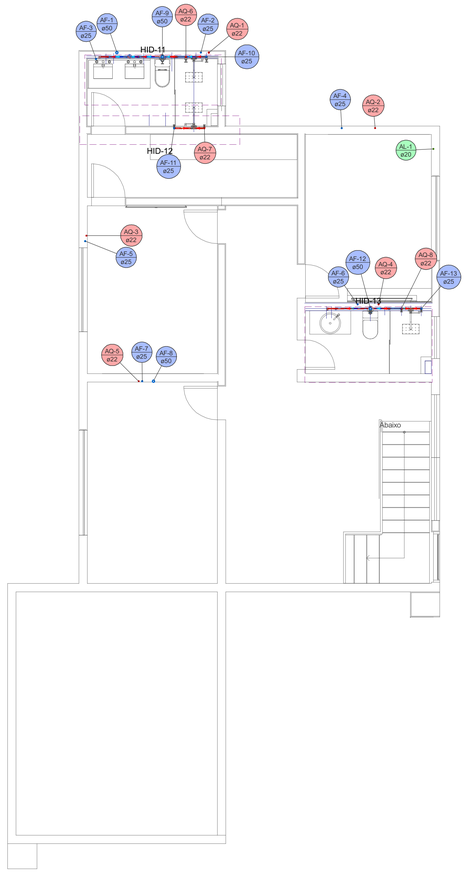

Lista de materiais - Superior	
Alimentação	
PVC rígido soldável	
Luva de correr p/ tubo	
20 mm	1 pç
Tubos	
20 mm	3.31 m
Água fria	
Aparelho	
Ducha higiênica	
25mm x 1/2"	2 pç
Torneira de lavatório	
25 mm - 1/2"	3 pç
Vaso Sanitário p/ Válvula de Descarga de 1 1/2"	
40mm - 1 1/2"	2 pç
Metais	
Registro Globo	
1.1/2"	1 pç
Registro de gaveta bruto ABNT	
3/4"	2 pç
Registro de gaveta c/ canopla cromada	
1.1/2"	1 pç
3/4"	1 pç
Válvula de descarga baixa pressão	
1.1/2"	2 pç
PVC Acessórios	
Bolsa de ligação p/ vaso sanitário	
1.1/2"	2 pç
Engate flexível plástico	
1/2 - 30cm	3 pç
Tubo de descarga VDE.	
38 mm	2 pç
Tubo de ligação latão cromado c/ canopla p/ vaso Sa.	
38 mm	2 pç
PVC rígido soldável	
Adapt sold curto c/bolsa-rosca p registro	
25 mm - 3/4	6 pç
50 mm - 1.1/2"	6 pç
Curva de transposição	
25 mm	3 pç
Joelho 90° soldável	
25 mm	5 pç
Luva de correr p/ tubo	
25 mm	5 pç
50 mm	4 pç
Luva soldável	
25 mm	4 pç
Tubos	
25 mm	31.72 m
50 mm	10.8 m
Tê 90 soldável	
25 mm	4 pç
PVC soldável azul c/ bucha latão	
Joelho de redução 90° soldável com bucha de latão	
25 mm- 1/2"	5 pç
Água quente	
Aparelho	
Chuveiro	
22mm x 3/4"	3 pç
CPVC Aquatherm	
Conector	
22 x 3/4"	6 pç
Curva de transposição	
22 mm	2 pç
Joelho 90	
22 mm	4 pç
Joelho 90° de transição	
22 x 1/2"	3 pç
22 x 3/4"	3 pç
Luva	
22 mm	5 pç
Luva de correr	
22 mm	3 pç
Tubo CPVC 3 Mts	
22 mm	28 m
28 mm	0.97 m
Tê 90	
22 mm	3 pç
Metais	
Registro de gaveta bruto ABNT	
3/4"	2 pç
Registro de gaveta c/ canopla cromada	
3/4"	1 pç
Registro monocomando para chuveiro	
3/4"	3 pç
PVC Acessórios	
Engate flexível cobre cromado com canopla	
1/2 - 30cm	3 pç
PVC rígido soldável	
Tê 90 soldável	
25 mm	1 pç

Legenda de condutos - Superior
Água fria
Água quente
Alimentação

Legenda - Superior
4 - Curva de transposição
2 - Registro bruto gaveta ABNT c/ CPVC
3 - Registro bruto gaveta ABNT c/PVC soldável
2 - Registro de gaveta c/canopla cromada c/ CPVC
3 - Registro de gaveta c/canopla cromada c/PVC soldável
3 - Registro globo c/ PVC soldável
3 - Registro monocomando
Valvula de descarga c/PVC soldável

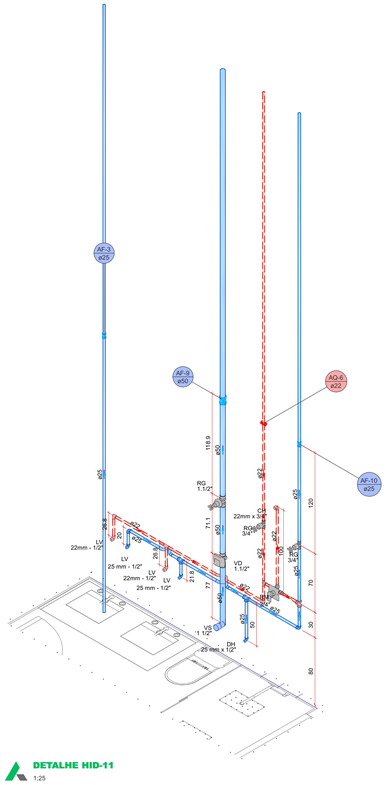

DETALHE HID-11
1:25

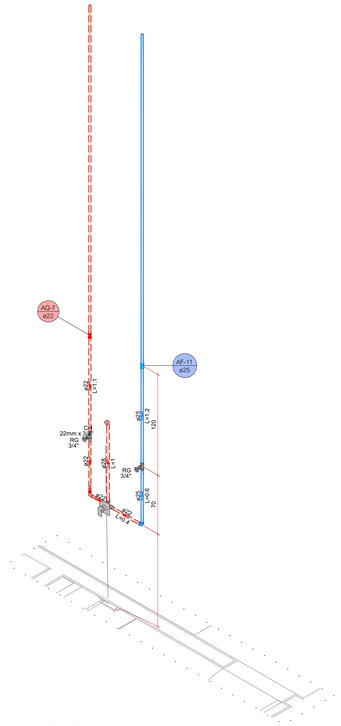

DETALHE HID-12
1:25

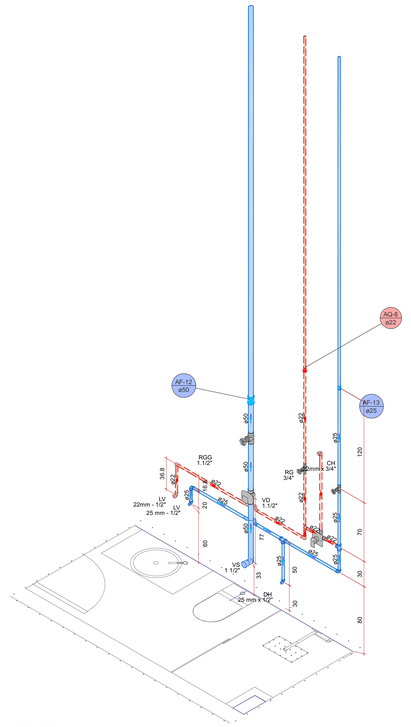

DETALHE HID-13
1:25

CONSTRU JÚNIOR
EMPRESA JÚNIOR DE ENGENHARIA CIVIL
AV. DOUTOR SÍLVIO MENICUCCI, S/N, DEP. DE ENGENHARIA (DEG),
CAMPUS DA UNIVERSIDADE FEDERAL DE LAVRAS, LAVRAS, MG.
CNPJ: 28.098.875/0001-97 TEL.: (35) 4104-4102 EMAIL: contato@construjr.com.br

TÍTULO: PROJETO HIDROSSANITÁRIO RESIDÊNCIAL

CONTEÚDO: HIDROSSANITÁRIO

LOGRADOURO: [redacted] ESCALA: 1/50

CLIENTE: [redacted] CPF/CNPJ: [redacted] DATA: 13/05/25

RESPONSÁVEL TÉCNICO: [redacted] CREA: [redacted] FOLHA: 01/

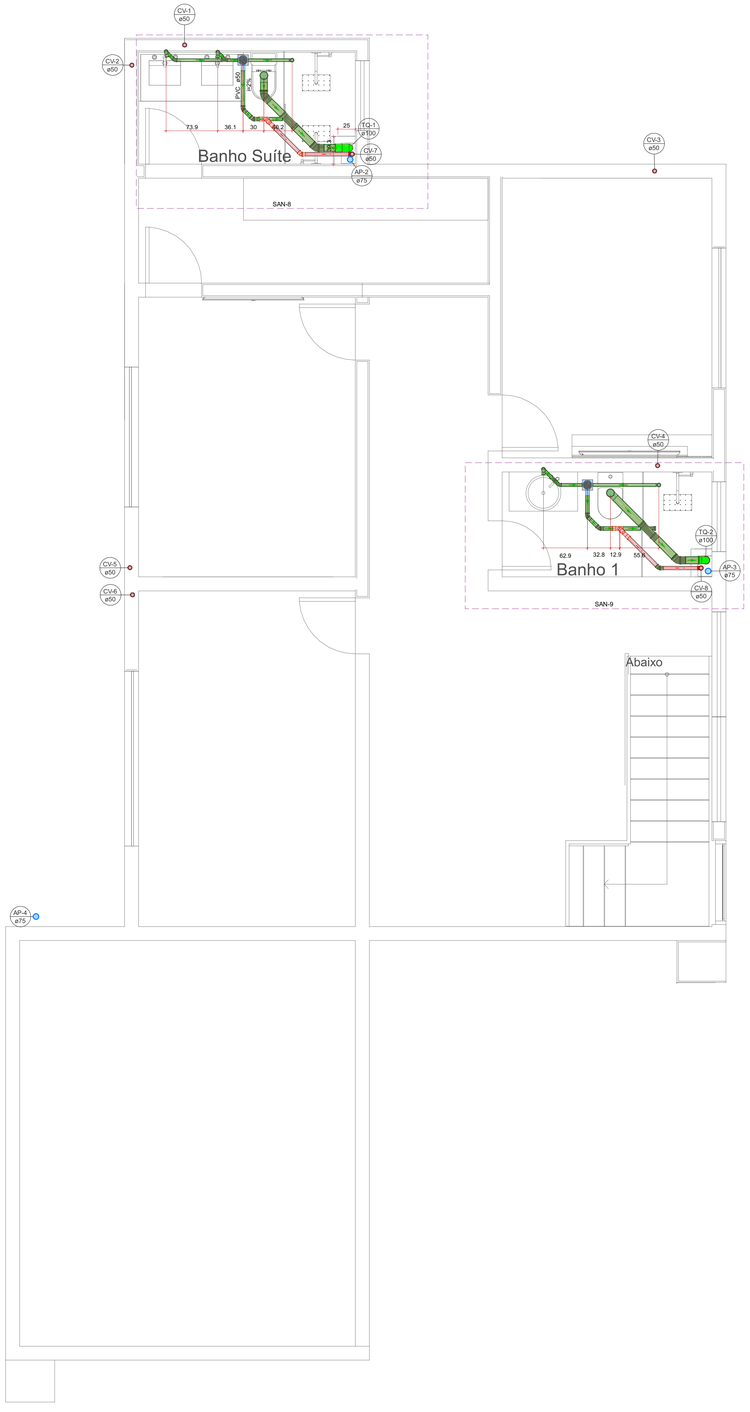

Legenda detalhada - Superior	
Caixa Sifonada	
PVC Acessórios	
Caixa sifonada	
150x150x50	1pç
PVC Esgoto	
Anel de borracha	
50mm - 2"	1pç
Chuveiro Residencial	
PVC Acessórios	
Ralo sifonado alt. reg. saída 40	
100 mm - 40 mm	1pç
PVC Esgoto	
Curva 90 curta	
40 mm	1pç
Joelho 45	
PVC Esgoto	
Anel de borracha	
100mm - 4"	1pç
Joelho 45	
100 mm	1pç
Joelho 45- desce	
PVC Esgoto	
Joelho 45	
40 mm	1pç
Joelho 90- coluna bolsa	
PVC Esgoto	
Anel de borracha	
50mm - 2"	1pç
Joelho 90	
50 mm	1pç
Joelho 90- desce	
PVC Esgoto	
Anel de borracha	
100mm - 4"	1pç
Joelho 90	
100 mm	1pç
Joelho 90- sobe	
PVC Esgoto	
Joelho 90	
40 mm	1pç
Junção invertida	
PVC Esgoto	
Anel de borracha	
100mm - 4"	1pç
50mm - 2"	1pç
Junção invertida	
100 mm x 50 mm	1pç
Junção simples	
PVC Esgoto	
Junção simples	
40 mm x 40 mm	1pç
Lavatório Residencial com sifão	
PVC Acessórios	
Sifão de copo p/ pia e lavatório	
1" - 1.1/2"	1pç
Válvula p/ lavatório e tanque	
1"	1pç
PVC Esgoto	
Curva 90 curta	
40 mm	1pç
Joelho 90 c/anel p/ esgoto secundário	
40 mm - 1.1/2"	1pç
Tubo rígido c/ ponta lisa	
40 mm	0.6m
Luva de correr- coluna	
PVC Esgoto	
Anel de borracha	
50mm - 2"	2pç
Luva de correr	
50 mm	1pç
Luva simples- coluna	
PVC Esgoto	
Anel de borracha	
75mm - 3"	1pç
Luva simples	
75 mm	1pç
Ramais de Ventilação	
PVC Esgoto	
Anel de borracha	
50mm - 2"	3pç
Joelho 90	
50 mm	1pç
Tê sanitário	
50 mm - 50 mm	1pç
Vaso Sanitário c/ J90°	
PVC Esgoto	
Anel de borracha	
100mm - 4"	1pç
Joelho 90	
100 mm	1pç
Vedação p/ saída de vaso sanitário	
100 mm	1pç
Vaso Sanitário c/ curva 90°	
PVC Esgoto	
Anel de borracha	
100mm - 4"	1pç
Curva 90 curta	
100 mm	1pç
Vedação p/ saída de vaso sanitário	
100 mm	1pç

Lista de materiais - Superior		
Esgoto		
PVC Acessórios		
Caixa sifonada		
150x150x50		1 pç
150x150x50R		1 pç
Ralo sifonado alt. reg. saída 40		
100 mm - 40 mm		2 pç
Sifão de copo p/ pia e lavatório		
1" - 1.1/2"		3 pç
Válvula p/ lavatório e tanque		
1"		3 pç
PVC Esgoto		
Anel de borracha		
100mm - 4"		9 pç
50mm - 2"		9 pç
Curva 90 curta		
100 mm		1 pç
40 mm		5 pç
Joelho 45		
100 mm		3 pç
40 mm		4 pç
50 mm		5 pç
Joelho 90		
100 mm		3 pç
40 mm		1 pç
Joelho 90 c/anel p/ esgoto secundário		
40 mm - 1.1/2"		3 pç
Junção invertida		
100 mm x 50 mm		2 pç
Junção simples		
40 mm x 40 mm		1 pç
Luva simples		
100 mm		2 pç
Tubo rígido c/ ponta lisa		
100 mm - 4"		9.51 m
40 mm		5.76 m
50 mm - 2"		2.06 m
Vedação p/ saída de vaso sanitário		
100 mm		2 pç
Pluvial		
Condutor pluvial		
Circular metálico		
75 mm		11.68 m
PVC Esgoto		
Anel de borracha		
75mm - 3"		5 pç
Luva de correr		
75 mm		2 pç
Luva simples		
75 mm		1 pç
Ventilação		
PVC Esgoto		
Anel de borracha		
50mm - 2"		21 pç
Joelho 45		
50 mm		1 pç
Joelho 90		
50 mm		4 pç
Luva de correr		
50 mm		6 pç
Tubo rígido c/ ponta lisa		
50 mm - 2"		23.22 m
Tê sanitário		
50 mm - 50 mm		2 pç

Legenda de condutos - Superior
Esgoto
Pluvial
Ventilação

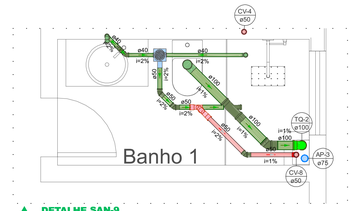

DETALHE SAN-9
1:25

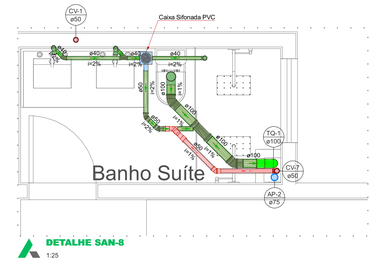

DETALHE SAN-8
1:25

OBSERVAÇÃO:TUBULAÇÕES DESVIANDO DAS VIGAS BALDRAMES

CONSTRU JÚNIOR

EMPRESA JÚNIOR DE ENGENHARIA CIVIL
Av. DOUTOR SÍLVIO MENICUCCI, S/N, DEP. DE ENGENHARIA (DEC),
CAMPUS DA UNIVERSIDADE FEDERAL DE LAVRAS, LAVRAS, MG
CNPJ: 28.098.875/0001-97 TEL.: (35) 4104-4102 EMAIL: contato@construjr.com.br

TÍTULO:	PROJETO HIDROSSANITÁRIO RESIDÊNCIAL
CONTEÚDO:	HIDROSSANITÁRIO
LOGRADOURO:	ESCALA: 1/50
CLIENTE: [redacted]	CPF/CNPJ: [redacted] DATA: 13/05/25
RESPONSÁVEL TÉCNICO: [redacted]	CREA: [redacted] FOLHA:

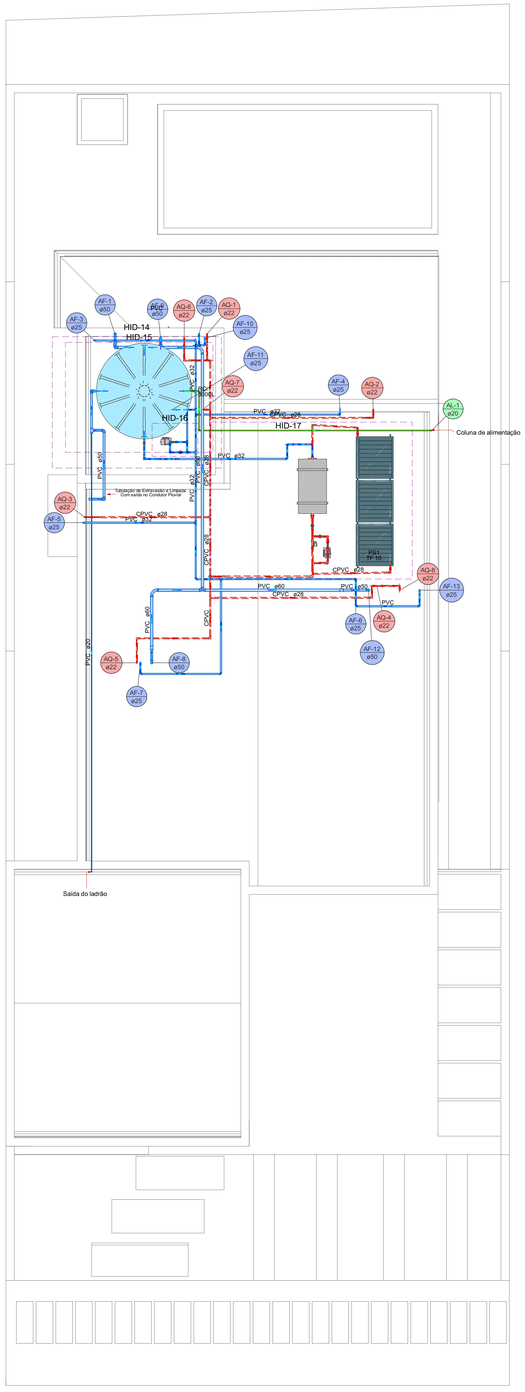

Legenda - Cobertura
R -Registro bruto gaveta ABNT c/ CPVC
R -Registro bruto gaveta ABNT c/PVC soldável
R -Registro de gaveta c/canopla cromada c/PVC soldável
R -Registro esfera VS compacto soldável

Legenda de condutos - Cobertura
Água fria
Água quente
Alimentação

Lista de materiais - Cobertura	
Alimentação	
Metais	
Registro de gaveta c/ canopla cromada 1/2"	1 pç
PVC rígido soldável	
Adapt.sold. c/ flange livre p/ cx. d' água 20 mm - 1/2"	1 pç
Adapt.sold.curto c/bolsa-rosca p registro 20 mm - 1/2"	2 pç
Joelho 90° soldável 50 mm	5 pç
Torneira de bóia 1"	1 pç
Tubos	
20 mm	13.26 m
Água fria	
Metais	
Registro de gaveta bruto ABNT 1"	1 pç
Registro de gaveta c/ canopla cromada 1"	1 pç
Registro esfera VS compacto soldável PVC 32 mm	1 pç
50 mm	1 pç
60 mm	1 pç
PVC rígido soldável	
Adapt.sold.c/ flange fixo p cx. d' água 32 mm - 1"	2 pç
50 mm - 1.1/2"	2 pç
60 mm - 2"	1 pç
Adapt.sold. longo c/ flange p/cx. d' agua 50 mm - 1.1/2"	1 pç
Adapt.sold.curto c/bolsa-rosca p registro 32 mm - 1"	5 pç
Bucha de redução sold. curta 32 mm - 25 mm	2 pç
60 mm - 50 mm	3 pç
Bucha de redução sold. longa 50 mm - 20 mm	1 pç
Cap soldável 32 mm	2 pç
Curva 90 soldável 60 mm	3 pç
Joelho 90° soldável 25 mm	2 pç
32 mm	24 pç
50 mm	9 pç
60 mm	1 pç
Joelho de redução 90 soldável 32 mm - 25 mm	7 pç
Luva de redução soldável 60 mm - 50 mm	1 pç
Luva soldável 32 mm	2 pç
60 mm	3 pç
Tubos	
20 mm	10.49 m
25 mm	36.83 m
32 mm	36.02 m
50 mm	31.03 m
60 mm	14.12 m
Tê 90 soldável 32 mm	9 pç
50 mm	2 pç
60 mm	3 pç
Tê de redução 90 soldável 32 mm - 25 mm	1 pç
Pressurizador	
Pressurizador Max Press 20E	1 pç
Reservatório climático	
Polietileno 3000 L	1 pç
Água quente	
CPVC Aquatherm	
Bucha de redução 28 x 22	6 pç
35 x 28	1 pç
Conector 28 x 1"	6 pç
35 x 1.1/4"	8 pç
54 x 2"	1 pç
Conector de transição 28 x 1"	2 pç
Filtro em Y 1"	1 pç
Joelho 90 22 mm	14 pç
28 mm	9 pç
35 mm	5 pç
Luva 28 mm	6 pç
35 mm	1 pç
Tubo CPVC 3 Mts 22 mm	36.42 m
28 mm	26.44 m
35 mm	4.67 m
Tê 90 22 mm	2 pç
28 mm	4 pç
35 mm	2 pç
Tê de Redução 28 x 22 mm	1 pç
Cobre	
Luva bolsa - bolsa 22 mm	1 pç
28 mm	2 pç
Metais	
Registro de gaveta bruto ABNT 1"r14	3 pç
Placa Solar	
MC 2000	
TF 10	1 pç
Pressurizador	
Pressurizador Max Press 20E	1 pç
Mini RW 12	1 pç
Reservatório térmico solar	
Reservatório Solar - Horizontal 300 L	1 pç

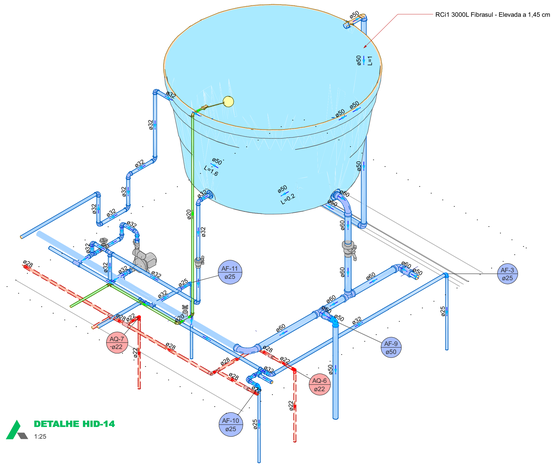

DETALHE HID-14
1:25

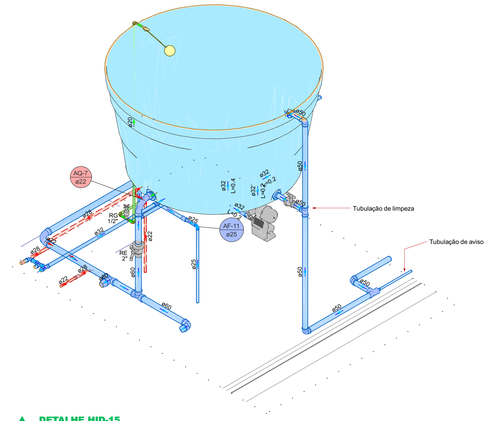

DETALHE HID-15
1:25

DETALHE HID-16
1:25

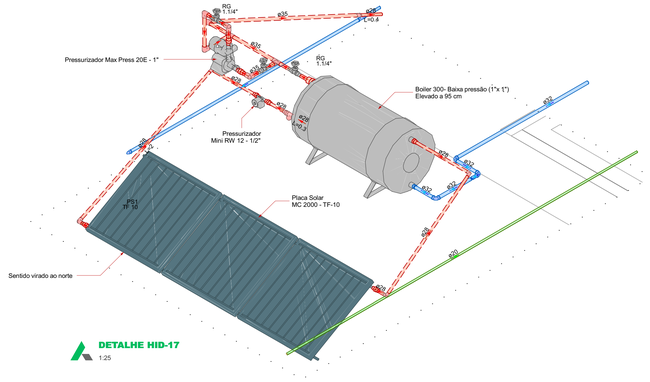

DETALHE HID-17
1:25

CONSTRU JÚNIOR

EMPRESA JÚNIOR DE ENGENHARIA CIVIL
AV. DOUTOR SÍLVIO MENICUCCI, S/N, DEP. DE ENGENHARIA (DEG),
CAMPUS DA UNIVERSIDADE FEDERAL DE LAVRAS, LAVRAS, MG.
CNPJ: 28.098.875/0001-97 TEL.: (35) 4104-4102 EMAIL: contato@construjr.com.br

TÍTULO:	PROJETO HIDROSSANITÁRIO RESIDÊNCIAL
CONTEÚDO:	HIDROSSANITÁRIO
LOGRADOURO: [redacted]	ESCALA: 1/50
CLIENTE: [redacted]	CPF/CNPJ: [redacted] DATA: 13/05/25
RESPONSÁVEL TÉCNICO: [redacted]	CREA: [redacted] FOLHA: 01/03

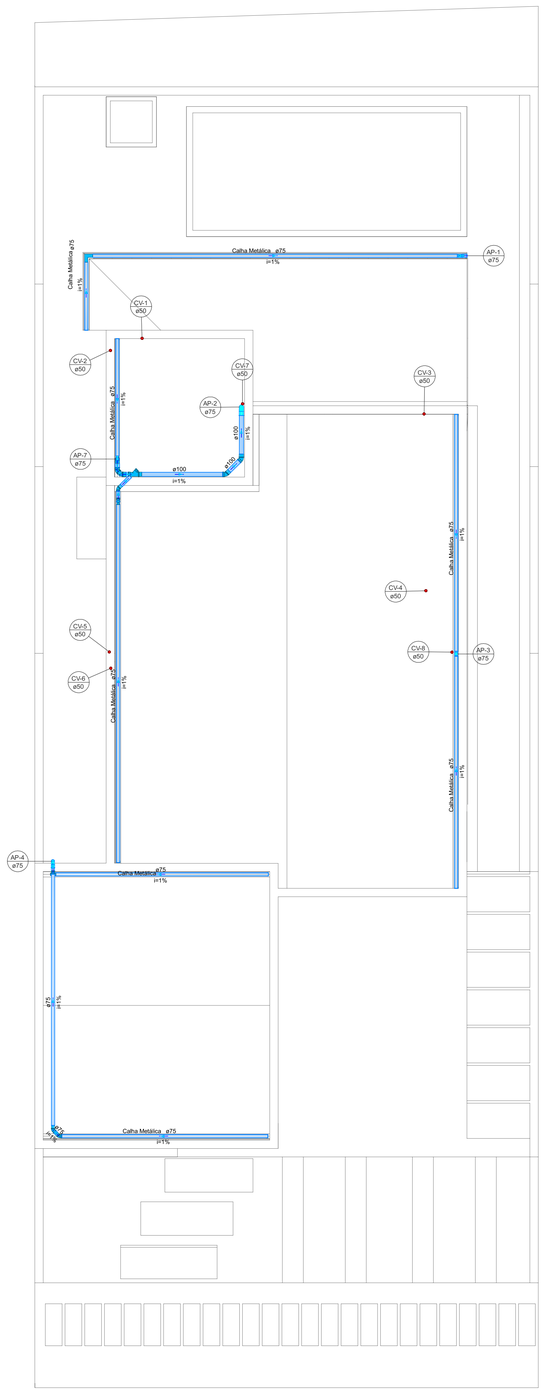

Legenda detalhada - Cobertura
Adaptador para bocal semi-circular c/ terminação
Calha metálica
Adaptador para bocal semi-circular — 75 mm x 75 mm — 1pç
Cabeceira semi-circular — 75 mm — 1pç
Adaptador para bocal semi-circular s/ terminação
Calha metálica
Adaptador para bocal semi-circular — 75 mm x 75 mm — 1pç
Cabeceira semi-circular
Calha metálica
Cabeceira semi-circular — 75 mm — 1pç
Curva 90 curta- coluna
PVC Esgoto
Anel de borracha — 100mm - 4" — 1pç
Anel de borracha — 75mm - 3" — 1pç
Curva 90 curta — 100 mm — 1pç
Redução excêntrica — 100 mm - 75 mm — 1pç
Curva 90 curta- coluna bolsa
PVC Esgoto
Anel de borracha — 75mm - 3" — 1pç
Curva 90 curta — 75 mm — 1pç
Curva 90 curta- desce
PVC Esgoto
Anel de borracha — 100mm - 4" — 1pç
Anel de borracha — 75mm - 3" — 1pç
Curva 90 curta — 100 mm — 1pç
Redução excêntrica — 100 mm - 75 mm — 1pç
Esquadro externo semi-circular
Calha metálica
Esquadro externo semi-circular — 75 mm — 1pç
Joelho 45
PVC Esgoto
Anel de borracha — 75mm - 3" — 1pç
Joelho 45 — 75 mm — 1pç
Joelho 90- desce
PVC Esgoto
Anel de borracha — 75mm - 3" — 1pç
Joelho 90 — 75 mm — 1pç
Junção invertida
PVC Esgoto
Anel de borracha — 100mm - 4" — 1pç
Anel de borracha — 75mm - 3" — 1pç
Junção invertida — 100 mm x 75 mm — 1pç
Terminal de ventilação- coluna
PVC Esgoto
Terminal de ventilação — 50 mm — 1pç

Lista de materiais - Cobertura		
Pluvial		
Calha metálica		
Adaptador para bocal semi-circular — 75 mm x 75 mm	5 pç	
Cabeceira semi-circular — 75 mm	11 pç	
Calha semi-circular — 75 mm	43.7 m	
Esquadro externo semi-circular — 75 mm	1 pç	
Condutor pluvial		
Circular metálico — 100 mm	4.17 m	
— 75 mm	33.77 m	
PVC Esgoto		
Anel de borracha — 100mm - 4"	7 pç	
— 75mm - 3"	9 pç	
Curva 90 curta — 100 mm	2 pç	
— 75 mm	1 pç	
Joelho 45 — 100 mm	4 pç	
— 75 mm	3 pç	
Joelho 90 — 75 mm	2 pç	
Junção invertida — 100 mm x 75 mm	1 pç	
Redução excêntrica — 100 mm - 75 mm	2 pç	
Ventilação		
PVC Esgoto		
Terminal de ventilação — 50 mm	8 pç	
Tubo rígido c/ ponta lisa — 50 mm - 2"	64.73 m	

Legenda de condutos - Cobertura
Pluvial
Ventilação

EMPRESA JÚNIOR DE ENGENHARIA CIVIL

AV. DOUTOR SÍLVIO MENICUCCI, S/N, DEP. DE ENGENHARIA (DEG),
CAMPUS DA UNIVERSIDADE FEDERAL DE LAVRAS, LAVRAS, MG.
CNPJ: 28.098.875/0001-97 TEL.: (35) 4104-4102 EMAIL: contato@construjr.com.br

TÍTULO: PROJETO HIDROSSANITÁRIO RESIDÊNCIAL

CONTEÚDO: HIDROSSANITÁRIO

LOGRADOURO: [redacted] ESCALA: 1/50

CLIENTE: [redacted] CPF/CNPJ: [redacted] DATA: 13/05/25

RESPONSÁVEL TÉCNICO: [redacted] CREA: [redacted] FOLHA: 03/03