

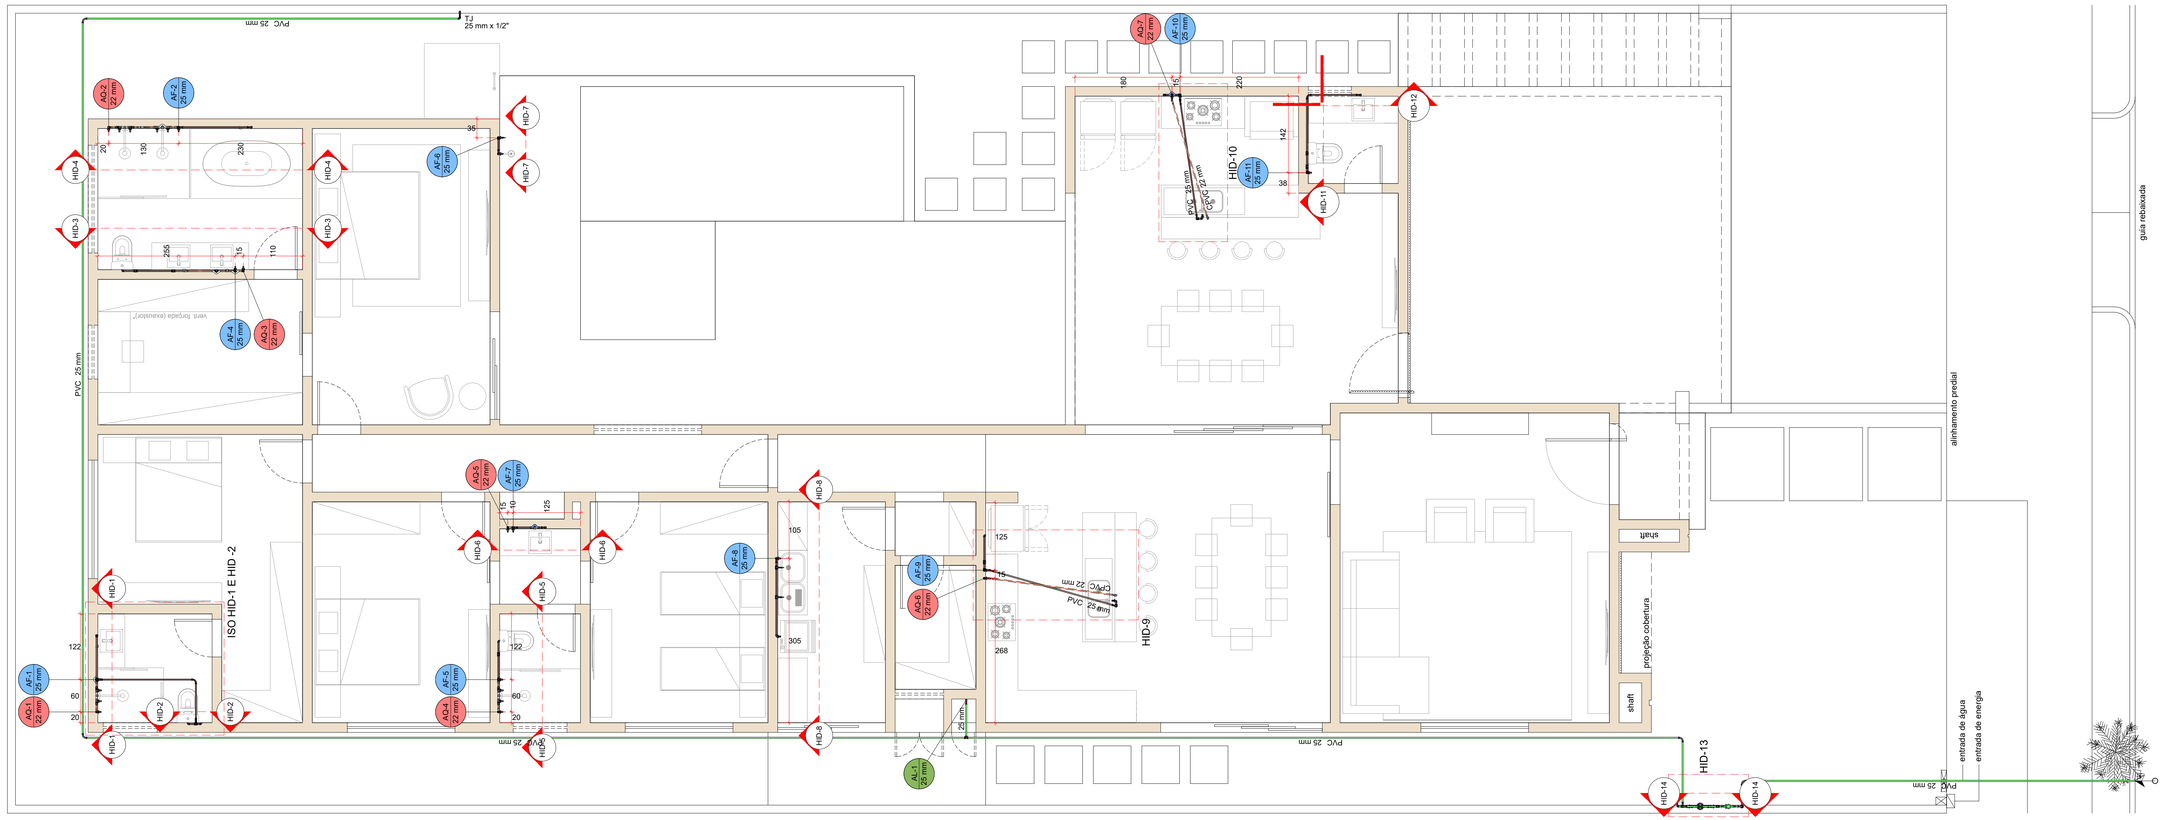


PLANTA BAIXA TÉRREO
Escala 1:50

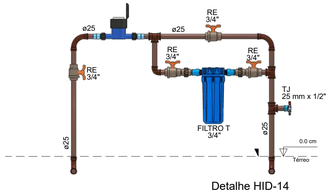

Detalhe HID-14
Escala 1:25

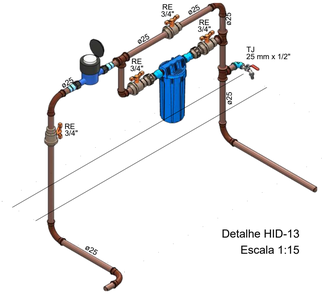

Detalhe HID-13
Escala 1:15

ESQUEMA DE LIGAÇÃO RP
ÁGUA QUENTE - TÊ MISTURADOR



ESQUEMA DE LIGAÇÃO RG
ÁGUA FRIA - PVC



ESQUEMA DE LIGAÇÃO RG
ÁGUA QUENTE - CPVC



Legenda de indicação	
AF-00 ø25	Coluna de Água Fria
AQ-00 ø25	Coluna de Água Quente
AL-00 ø25	Coluna de Alimentação
AR-00 ø100	Coluna de Água de Reuso
RA-00 ø100	Retorno de Água Quente
ALP-00 ø100	Coluna Poço Artesiano

AF-00 ø25 — Indicação da coluna / Número da coluna / Diâmetro da coluna

Legenda de peças	
DH	Ducha Higiênica
LV	Lavatório
FTA	Filtro de Água
RG	Registro de Gaveta
RE	Registro de Esfera
TLR	Tanque de Lavar Roupa
VS	Vaso Sanitário
RP	Registro de Pressão
CH	Chuveiro
MLR	Máquina de Lavar Roupa
PIA	Pia de Cozinha
RM	Registro Monocomando
TJ	Torneira de Jardim

Legenda de condutos
Água Fria
Água Quente
Alimentação Rua
Água Reuso
Retorno Água Quente
Água Poço Artesiano

PROJETO HIDROSSANITÁRIO RESIDENCIAL

EXECUTIVO HIDRÁULICO

CONTEÚDO DA PRANCHA:
PLANTA BAIXA E DETALHES

AUTOR:
VICTOR HUGO CARVALHO - ENGENHEIRO CIVIL


FOLHA:
01/06

ORIGEM:
PROJETO DESENVOLVIDO EM CURSO DE CAPACITAÇÃO


DATA:
ABRIL/2024

FINALIDADE: OBRA RESIDENCIAL
Dados do proprietário e endereço preservados


ESCALA:
INDICADA

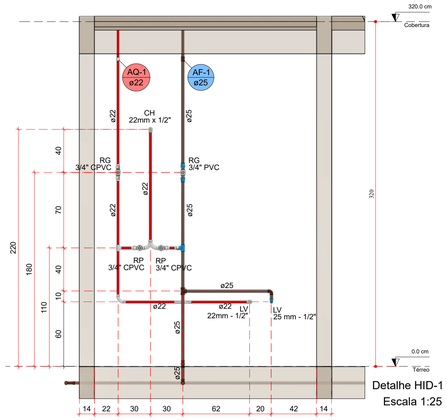


Detalhe HID-1
Escala 1:25

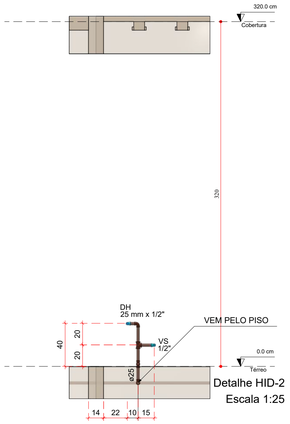


Detalhe HID-2
Escala 1:25

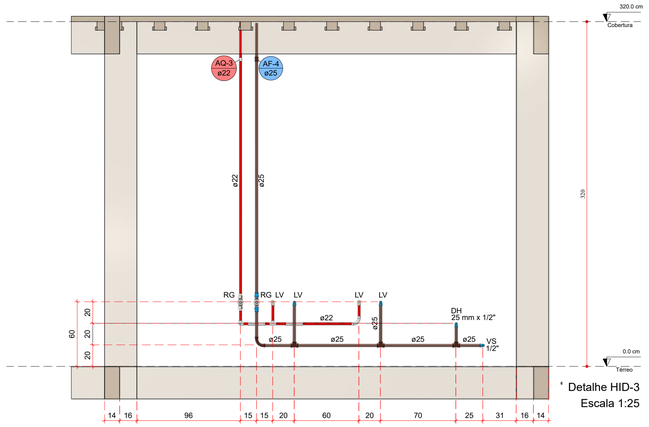


Detalhe HID-3
Escala 1:25

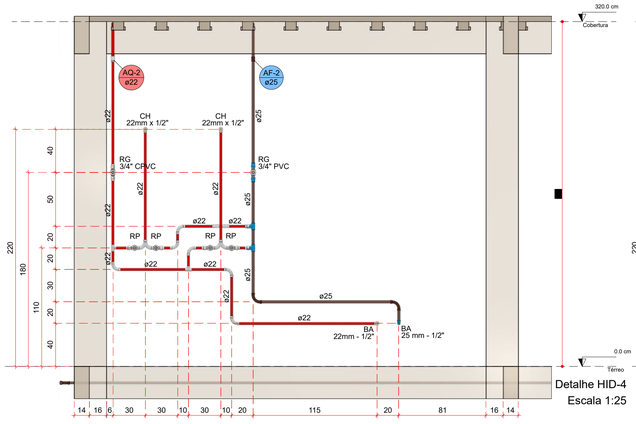


Detalhe HID-4
Escala 1:25

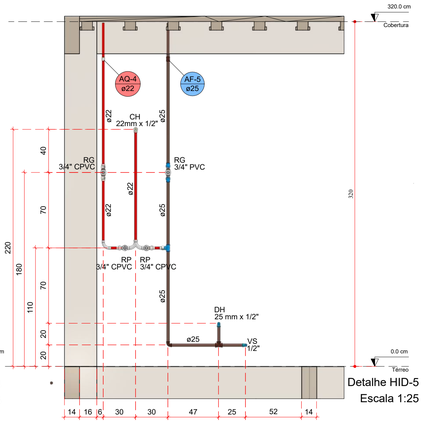


Detalhe HID-5
Escala 1:25

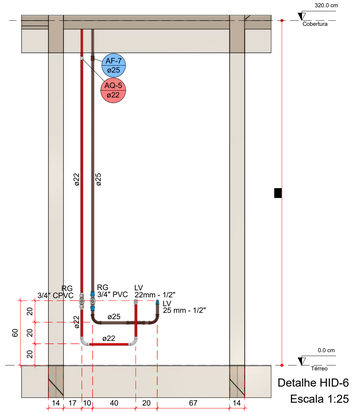


Detalhe HID-6
Escala 1:25

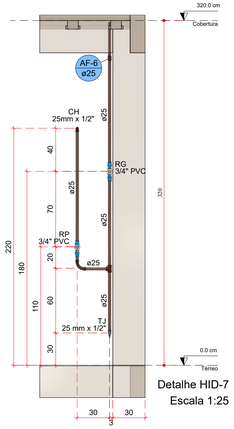


Detalhe HID-7
Escala 1:25

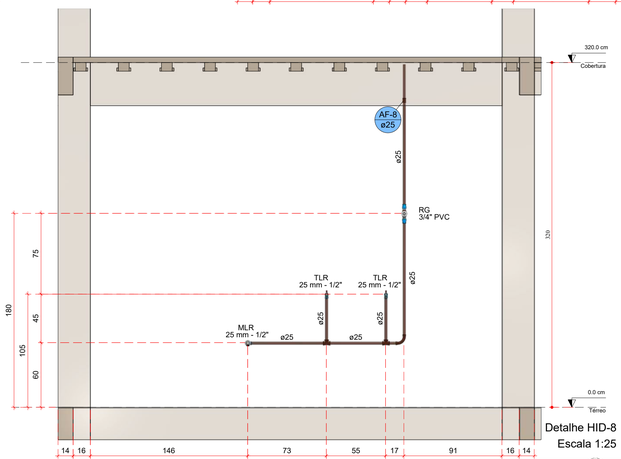


Detalhe HID-8
Escala 1:25

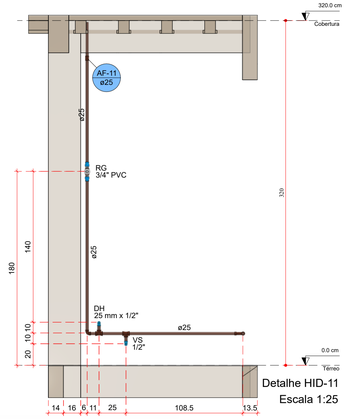


Detalhe HID-11
Escala 1:25

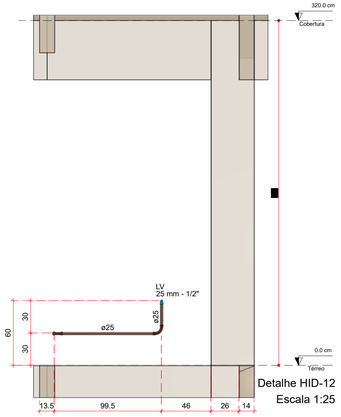


Detalhe HID-12
Escala 1:25

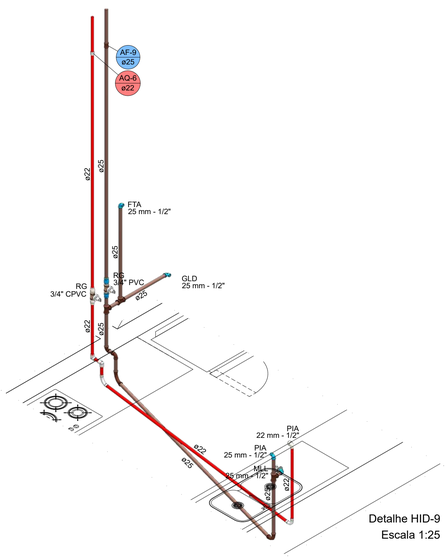

Detalhe HID-9
Escala 1:25

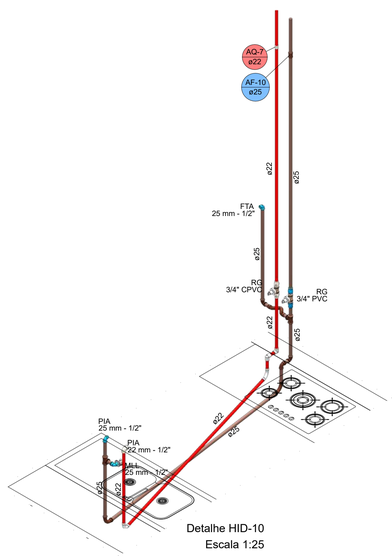

Detalhe HID-10
Escala 1:25

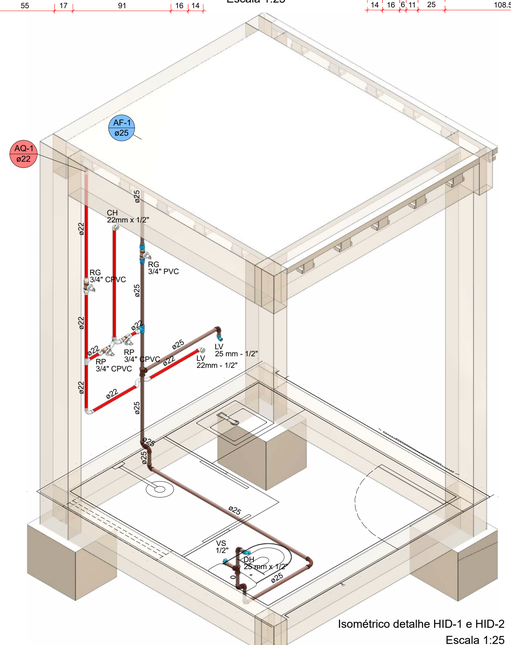

Isométrico detalhe HID-1 e HID-2
Escala 1:25

ESQUEMA DE LIGAÇÃO RG ÁGUA QUENTE - CPVC



ESQUEMA DE LIGAÇÃO RP ÁGUA QUENTE - TÊ MISTURADOR



ESQUEMA DE LIGAÇÃO RG ÁGUA FRIA - PVC



Legenda de indicação	
AF-00 ø25	Coluna de Água Fria
AQ-00 ø25	Coluna de Água Quente
AL-00 ø25	Coluna de Alimentação
AR-00 ø100	Coluna de Água de Reuso
RA-00 ø100	Retorno de Água Quente
ALP-0 ø100	
AF-00 ø25	

Legenda de peças	
DH	Ducha Higiênica
LV	Lavatório
FTA	Filtro de Água
RG	Registro de Gaveta
RE	Registro de Esfera
TLR	Tanque de Lavar Roupa
VS	Vaso Sanitário
RP	Registro de Pressão
CH	Chuveiro
MLR	Máquina de Lavar Roupa
PIA	Pia de Cozinha
RM	Registro Monocomando

Legenda de condutos
Água Fria
Água Quente
Alimentação Rua
Água Reuso
Retorno Água Quente

PROJETO HIDROSSANITÁRIO RESIDENCIAL

EXECUTIVO HIDRÁULICO

CONTEÚDO DA PRANCHA:
PLANTA BAIXA E DETALHES

AUTOR:
VICTOR HUGO CARVALHO - ENGENHEIRO CIVIL


FOLHA:
02/06

ORIGEM:
PROJETO DESENVOLVIDO EM CURSO DE CAPACITAÇÃO


DATA:
ABRIL/2024

FINALIDADE: OBRA RESIDENCIAL
Dados do proprietário e endereço preservados

ESCALA:
INDICADA

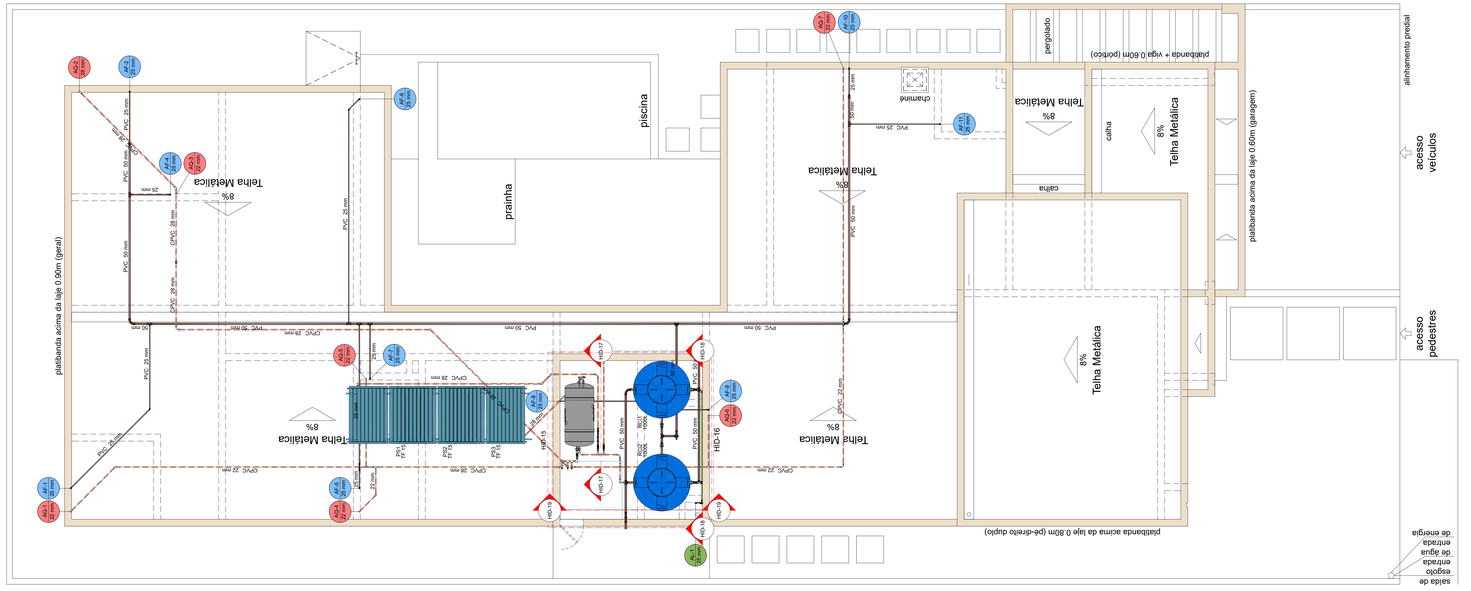

PLANTA BAIXA COBERTURA
Escala 1:50

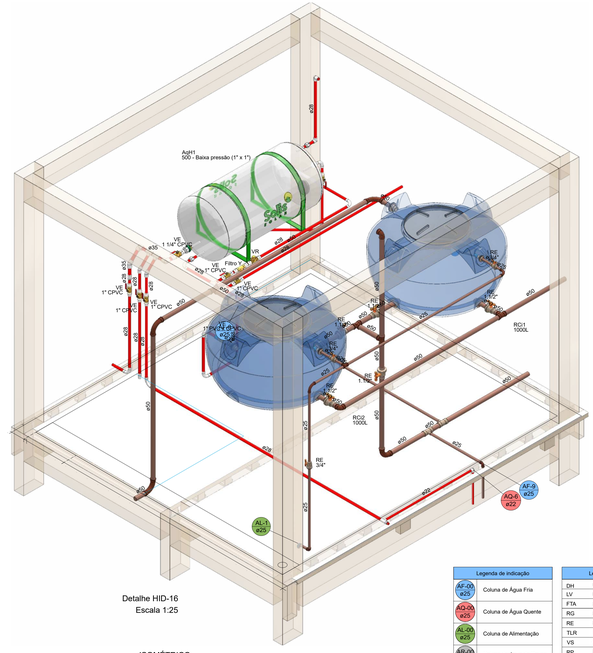

Detalhe HID-16
Escala 1:25


ISOMÉTRICO
Escala 1:25

Legenda de indicação	
AF-2 ø25	Coluna de Água Fria
AQ-2 ø25	Coluna de Água Quente
AL-2 ø25	Coluna de Alimentação
AR-2 ø100	Coluna de Água de Reuso
AAQ-2 ø100	Retorno de Água Quente
ALF-2 ø100	Coluna


Legenda de peças	
DH	Ducha Higiênica
LV	Lavatório
FTA	Filtro de Água
RG	Registro de Gaveta
RE	Registro de Esfera
TLR	Tanque de Lavar Roupa
VS	Vaso Sanitário
RP	Registro de Pressão
CH	Chuveiro
MLR	Máquina de Lavar Roupa
PIA	Pia de Cozinha
RM	Registro Monocomando

Legenda de condutos	
Água Fria	
Água Quente	
Alimentação Rua	
Água Reuso	
Retorno Água Quente	


AF-2 ø25 — Indicaç / Número / Diâmet

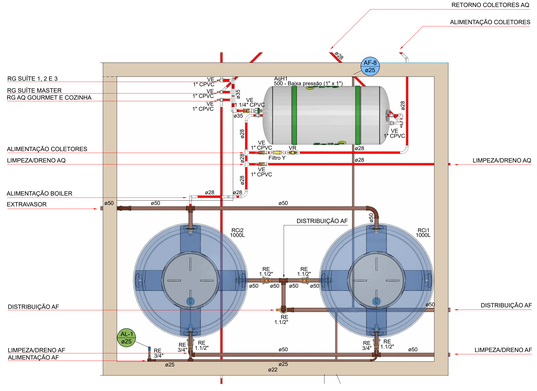


Detalhe HID-15
Escala 1:25

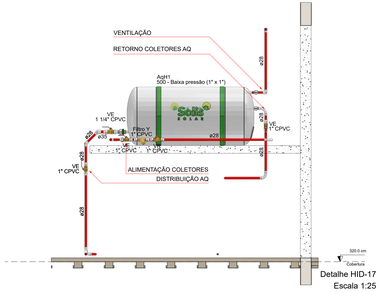

Detalhe HID-17
Escala 1:25

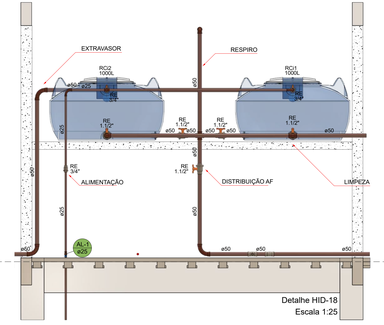

Detalhe HID-18
Escala 1:25

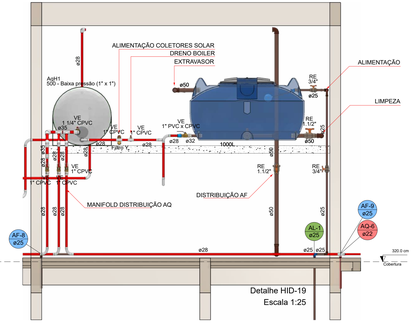

Detalhe HID-19
Escala 1:25

PROJETO HIDROSSANITÁRIO RESIDENCIAL

EXECUTIVO HIDRÁULICO

CONTEÚDO DA PRANCHA:
PLANTA BAIXA E DETALHES

AUTOR:
VICTOR HUGO CARVALHO - ENGENHEIRO CIVIL


FOLHA:
03/06

ORIGEM:
PROJETO DESENVOLVIDO EM CURSO DE CAPACITAÇÃO


DATA:
ABRIL/2024

FINALIDADE: OBRA RESIDENCIAL
Dados do proprietário e endereço preservados

ESCALA:
INDICADA

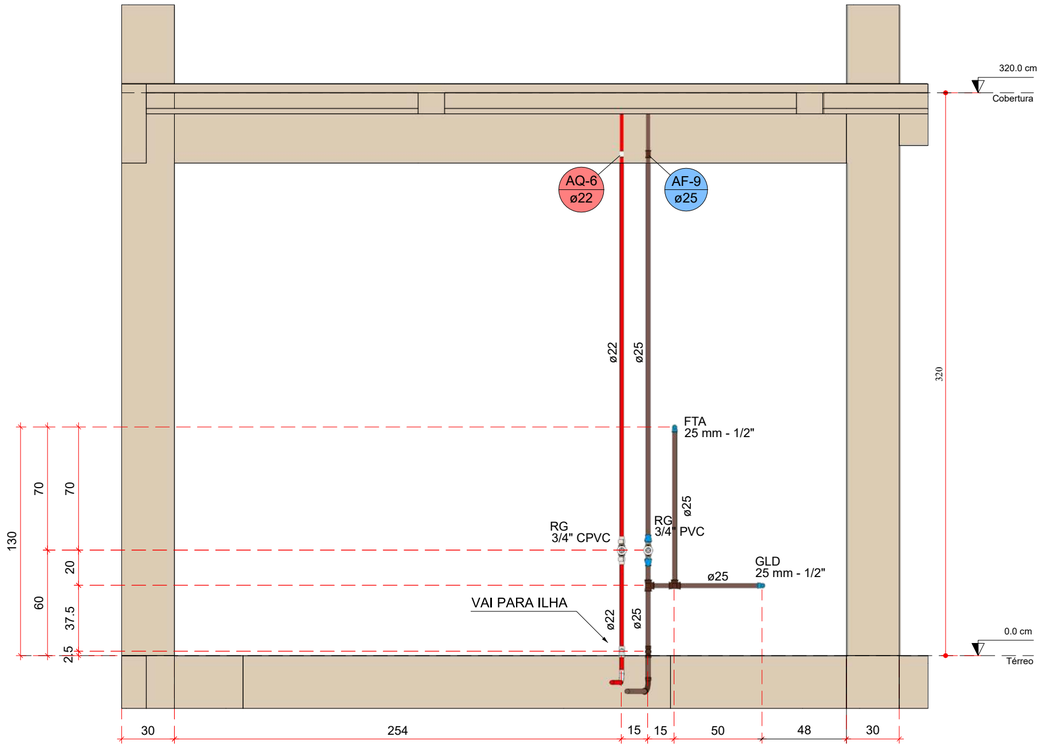

Detalhe HID-16
Escala 1:25

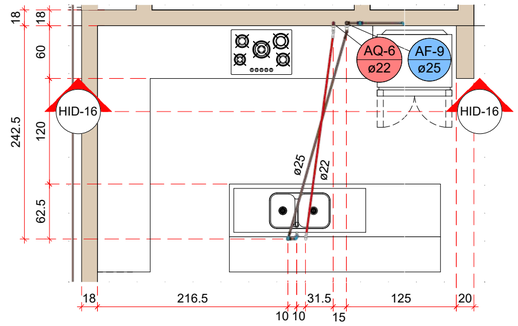

Detalhe Planta Cozinha
Escala 1:50

ESQUEMA DE LIGAÇÃO RG
ÁGUA QUENTE - CPVC



ESQUEMA DE LIGAÇÃO RG
ÁGUA FRIA - PVC




Legenda de indicação	
AF-00 ø25	Coluna de Água Fria
AQ-00 ø25	Coluna de Água Quente
AL-00 ø25	Coluna de Alimentação
AR-00 ø100	Coluna de Água de Reuso
RA-00	Retorno de Água Quente


Legenda de peças	
DH	Ducha Higiênica
LV	Lavatório
FTA	Filtro de Água
RG	Registro de Gaveta
RE	Registro de Esfera
TLR	Tanque de Lavar Roupa
VS	Vaso Sanitário
RP	Registro de Pressão
CH	Chuveiro
MLR	Máquina de Lavar Roupa

Legenda de condutos
Água Fria
Água Quente
Alimentação Rua
Água Reuso
Retorno Água Quente

A

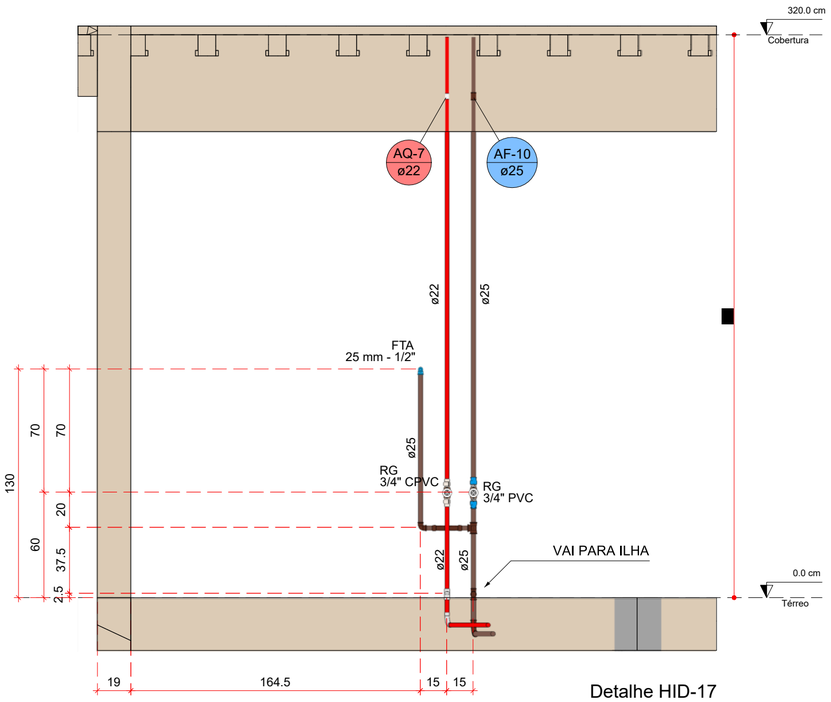

Detalhe HID-17
Escala 1:25

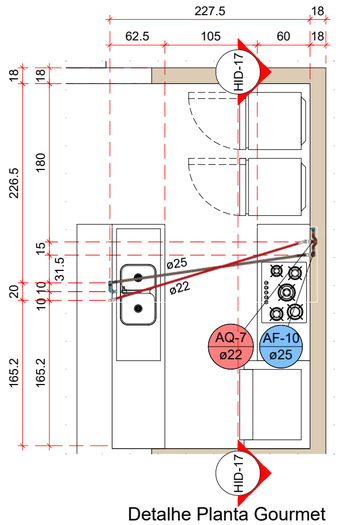


Detalhe Planta Gourmet
Escala 1:50

PROJETO HIDROSSANITÁRIO RESIDENCIAL


EXECUTIVO HIDRÁULICO

CONTEÚDO DA PRANCHA:
PLANTA EXTRA DE REVISÃO

AUTOR:	FOLHA:
VICTOR HUGO CARVALHO - ENGENHEIRO CIVIL	**04/06**
ORIGEM: PROJETO DESENVOLVIDO EM CURSO DE CAPACITAÇÃO	DATA: AGO/2024
FINALIDADE: OBRA RESIDENCIAL Dados do proprietário e endereço preservados	ESCALA: INDICADA

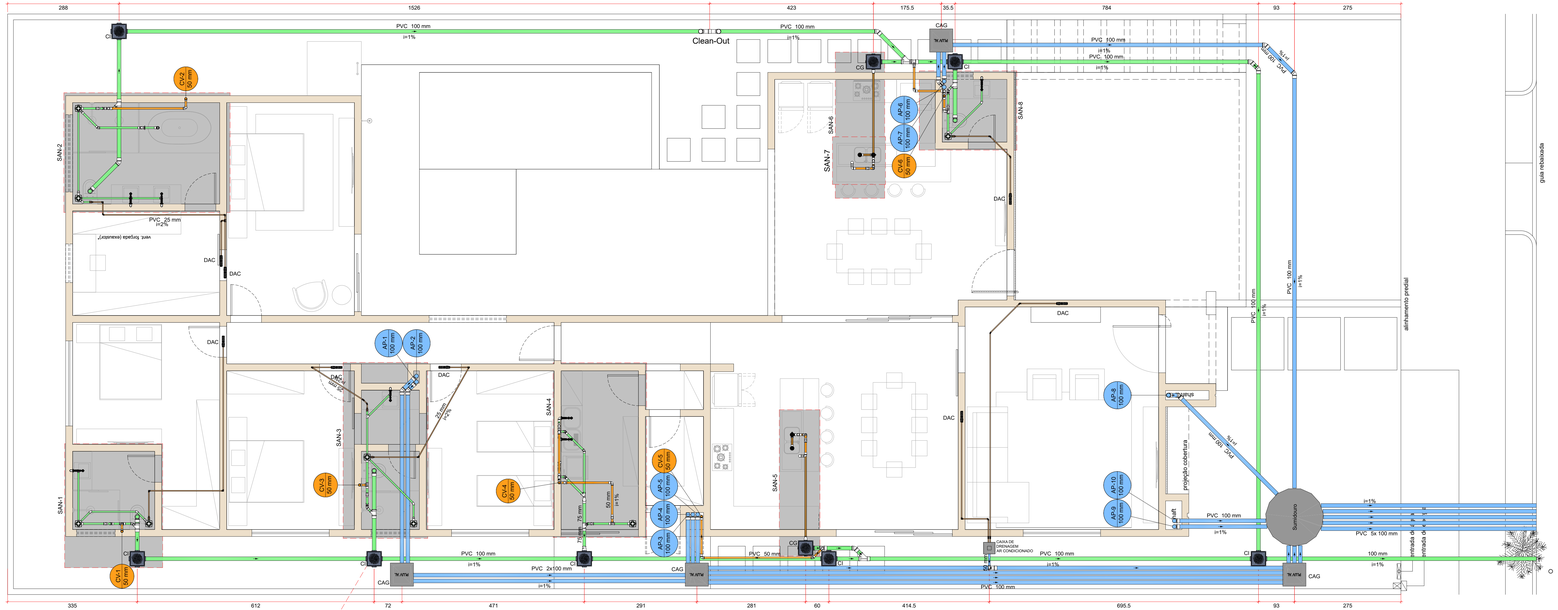


PLANTA BAIXA TÉRREO
Escala 1:50

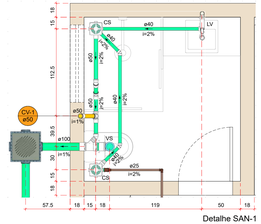


Detalhe SAN-1
Escala 1:25



Tampa Reforçada

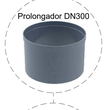
Prolongador DN300


Caixa de Inspeção

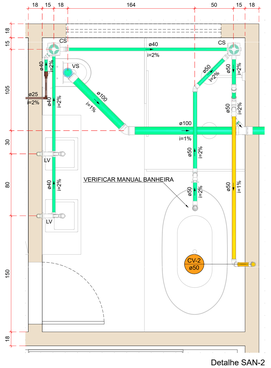


Detalhe SAN-2
Escala 1:25

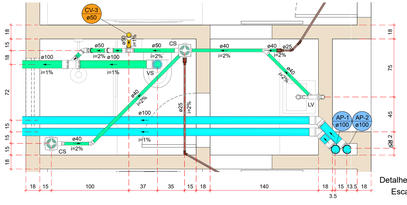

Detalhe SAN-3
Escala 1:25




Detalhe SAN-5
Escala 1:25

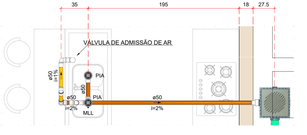


Detalhe SAN-6
Escala 1:25


Legenda de peças - Térreo		
	PVC Esgoto	
E2	Bucha de redução longa 50 mm - 40 mm	1pç
E3	PVC Esgoto Adaptador para Válvula Americana 40mm x 1 1/2"	1pç
E4	PVC Esgoto Válvula de Pia Americana 1 1/2"	1pç
E5	Sifão Expert Curva 90 curta 50 mm Joelho 90 50 mm Luva simples 50 mm Tê sanitário 50 mm - 50 mm	2pç 1pç 1pç 1pç 1pç
E6	PVC Esgoto Adaptador MLL Astra 1 1/2"	1pç
E7	PVC Esgoto Anel de borracha 50mm - 2" Tê sanitário 50 mm - 50 mm	2pç 1pç
V1	PVC Esgoto Válvula de Admissão de Ar 50 mm	1pç
V8	PVC Esgoto Tê de inspeção 50 mm - 50 mm	1pç

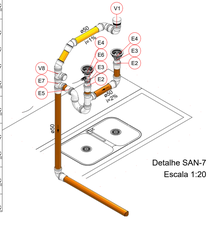

Detalhe SAN-7
Escala 1:20

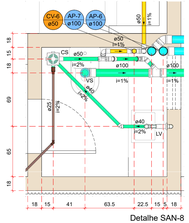

Detalhe SAN-8
Escala 1:25

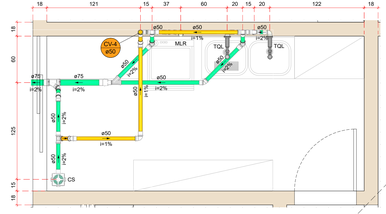


Detalhe SAN-4
Escala 1:25



Det. Execução Clean-Out
Escala 1:25




Det. Execução Clean-Out
Escala 1:25

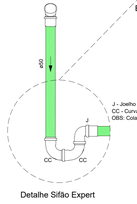

J - Joelho 90°
CC - Curva Curta 90°
OBS: Colar as peças

Detalhe Sifão Expert

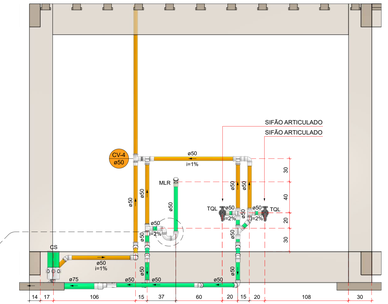

Detalhe C SAN-4
Escala 1:25

Sifão Flexível




Sifão Articulado



Detalhes - Caixa de Gordura Pequena (CGP) - 18 Litros - TIGRE



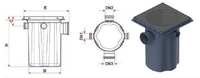

Cotas	Dimensões (mm)
C	55
D	295
DN1	50
DN2	75
DN3	100
E	392
H	449

Legenda de indicação	
TQ-01 ø100	Coluna de Esgoto Primário
TQ-02 ø150	Coluna de Esgoto Gordura
AP-01 ø100	Coluna de Águas Pluviais
CV-01 ø100	Coluna de Ventilação
	Indicação da coluna
TQ-01 ø150	Número da coluna
	Diâmet

Legenda de peças	
CAG	Caixa de Areia c/ Grelha
CI	Caixa de Inspeção
CG	Caixa de Gordura
CS	Caixa Sifonada c/ Ralo
DAC	Dreno de Ar Condicionado
LV	Lavatório
MLL	Máquina de Lavar Louça
MLR	Máquina de Lavar Roupa
PIA	Pia de Cozinha

Legenda de condutos	
	Esgoto
	Dreno Ar Condicionado
	Esgoto (Gordura PVC Serie R)
	Esgoto (Prolongador)
	Pluvial

E

PROJETO HIDROSSANITÁRIO RESIDENCIAL

EXECUTIVO SANITÁRIO

CONTEÚDO DA PRANCHA:
PLANTA BAIXA TÉRREO E DETALHES

AUTOR:
VICTOR HUGO CARVALHO - ENGENHEIRO CIVIL


FOLHA:
05/06

ORIGEM:
PROJETO DESENVOLVIDO EM CURSO DE CAPACITAÇÃO

DATA:
ABRIL/2024

FINALIDADE: OBRA RESIDENCIAL
Dados do proprietário e endereço preservados

ESCALA:
INDICADA

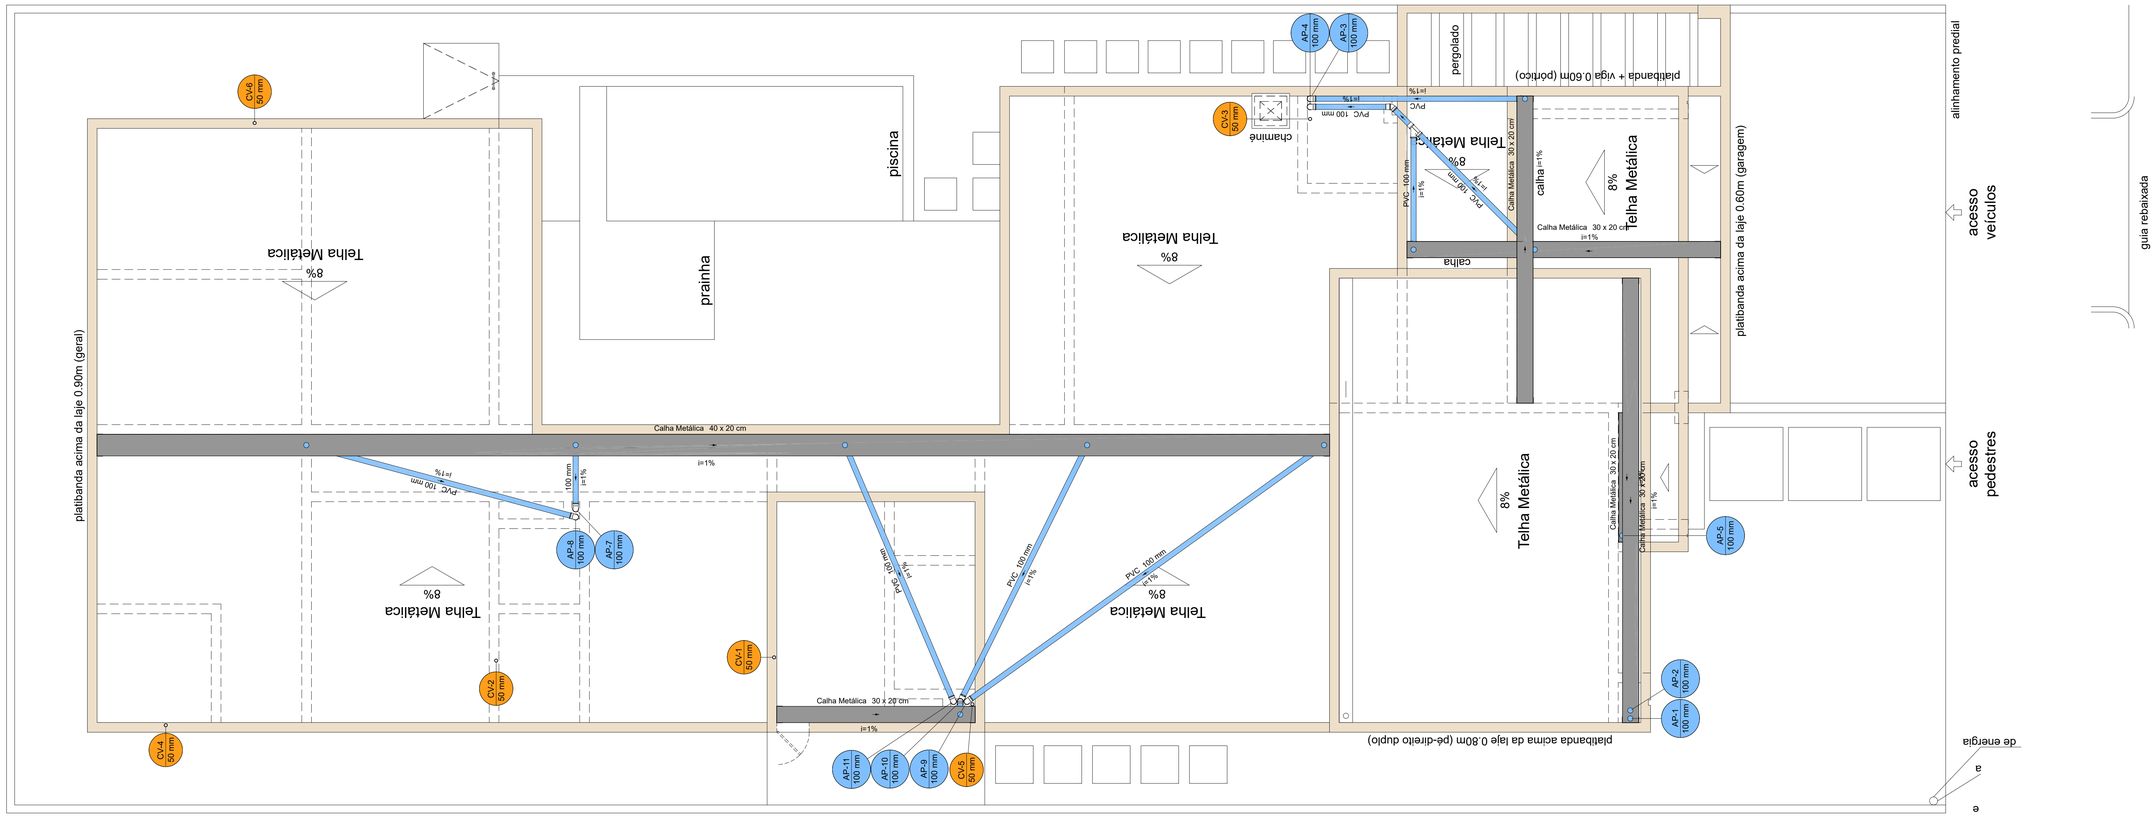

Legenda de indicação	
TQ-00 ø100	Coluna de Esgoto Primário
TG-00 ø100	Coluna de Esgoto Gordura
AP-00 ø100	Coluna de Águas Pluviais
CV-00 ø100	Coluna de Ventilação
TQ-00 ø100	Indicação da coluna Número da coluna Diâmetro da coluna

Legenda de peças	
CAG	Caixa de Areia c/ Grelha
CI	Caixa de Inspeção
CG	Caixa de Gordura
CS	Caixa Sifonada c/ Ralo
DAC	Dreno de Ar Condicionado
LV	Lavatório
MLL	Máquina de Lavar Louça
MLR	Máquina de Lavar Roupa
PIA	Pia de Cozinha
RL	Ralo Linear
TQL	Tanque de Lavar
VS	Vaso Sanitário

Legenda de condutos
Esgoto
Dreno Ar Condicionado
Esgoto (Gordura PVC Serie R)
Esgoto (Prolongador)
Pluvial
Ventilação

PROJETO HIDROSSANITÁRIO RESIDENCIAL

EXECUTIVO SANITÁRIO

CONTEÚDO DA PRANCHA:
PLANTA BAIXA COBERTURA

AUTOR:
VICTOR HUGO CARVALHO - ENGENHEIRO CIVIL

FOLHA:
06/06

ORIGEM:
PROJETO DESENVOLVIDO EM CURSO DE CAPACITAÇÃO

DATA:
ABRIL/2024

FINALIDADE: OBRA RESIDENCIAL
Dados do proprietário e endereço preservados

ESCALA:
INDICADA